
1階 平面計画図（受付・待合・診察室・処置室）

貸室面積 98.36㎡（約29.75坪）

← 正面道路（Y1通り・歩道）

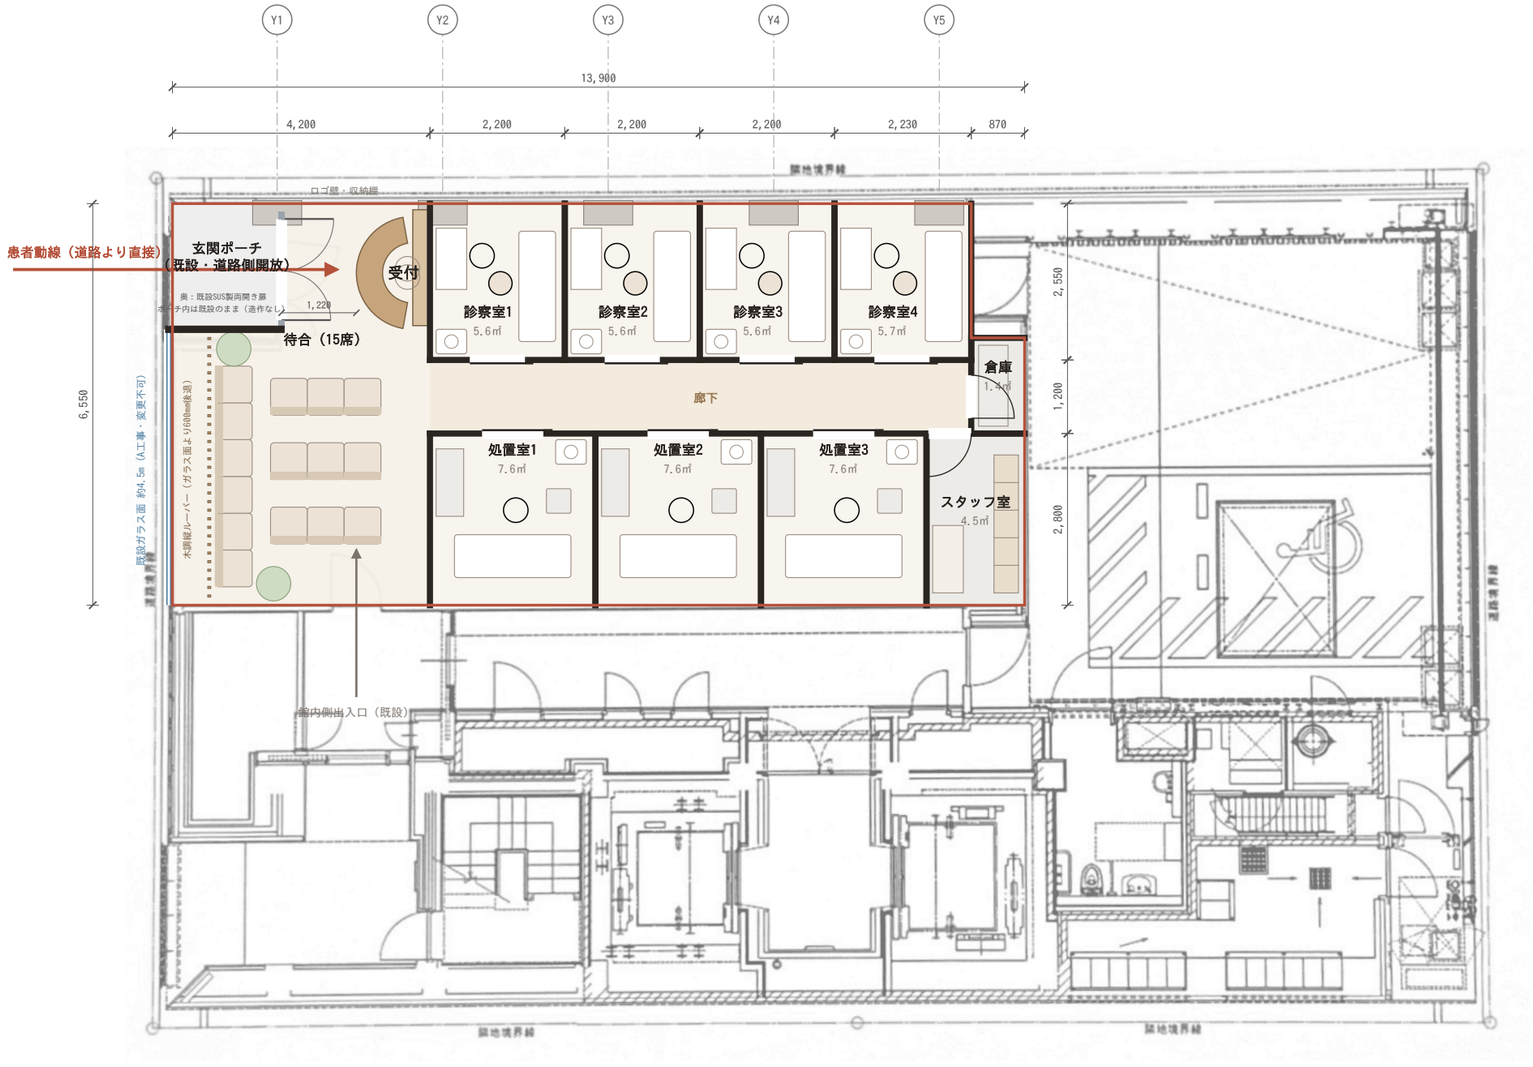

図の向き

左：正面道路（Y1側）
上：X1通り側　※真北は要確認

- 貸室 98.36㎡（約29.75坪）
- 診察室・処置室
- 廊下
- スタッフ室・倉庫
- 玄関ポーチ（既設・区画内）

諸室面積表（内法・概算）

診察室1	5.6㎡
診察室2	5.6㎡
診察室3	5.6㎡
診察室4	5.7㎡
処置室1	7.6㎡
処置室2	7.6㎡
処置室3	7.6㎡
スタッフ室	4.5㎡
倉庫	1.4㎡

・下図（グレー）は貸主提供の募集図面（1階 店舗区画）。赤線＝貸室区画（98.36㎡）、着色部・室配置が当社計画（C工事）。
・部屋構成：受付、待合（最大15名・15席）、診察室4室（各約5.6㎡）、処置室3室（各約7.6㎡）、スタッフ室・倉庫。診察室・処置室は全室に手洗い器。
・受付は玄関の既設扉の正面（扉から1,220mm）。待合は道路側ガラス面に面し、廊下（幅1,200）から診察室・処置室へ。館内側出入口からも廊下へ直接つながる。
・玄関ポーチ（道路側開放）・奥の既設SUS両開き扉・道路側ガラス面（約4.5m）は既設（A工事）のまま。ガラス面から600mm内側に木調縦ルーバー、600mm以内に造作・サインなし（内装マニュアル7-(7)）。
・トイレは館内共用トイレを利用。間仕切・内装材は全て不燃材、カーペットは防炎品。

整形外科ふっか／整痛院ふっか 東京駅院 出店計画 ／ 日本橋WASAMIビル


1階 平面計画図（受付・待合・診察室・処置室）

基本計画（出店企画書添付資料）　2026.10

S=1/100


No.A-01　A3

外観立面図・サイン計画図（正面 Y1通り）

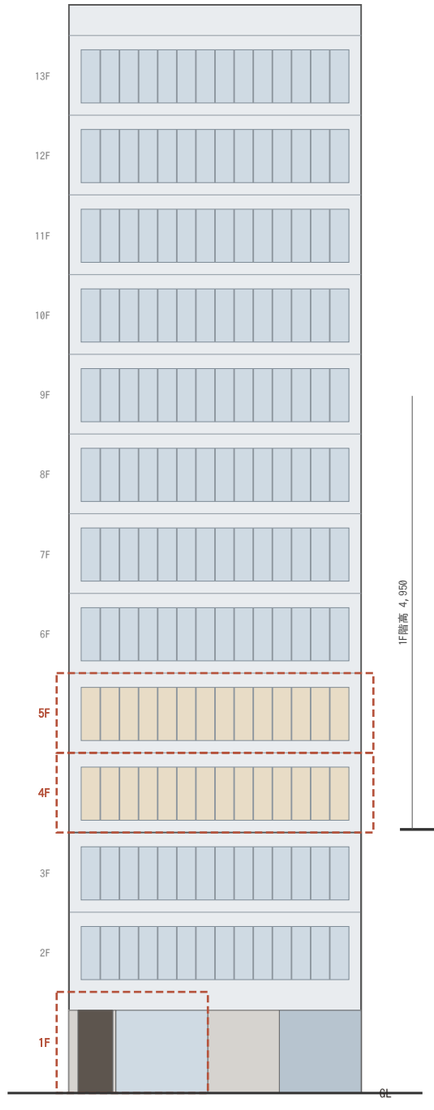

正面全体立面（Y1通り・模式）

S=1/300　赤破線＝当社区画

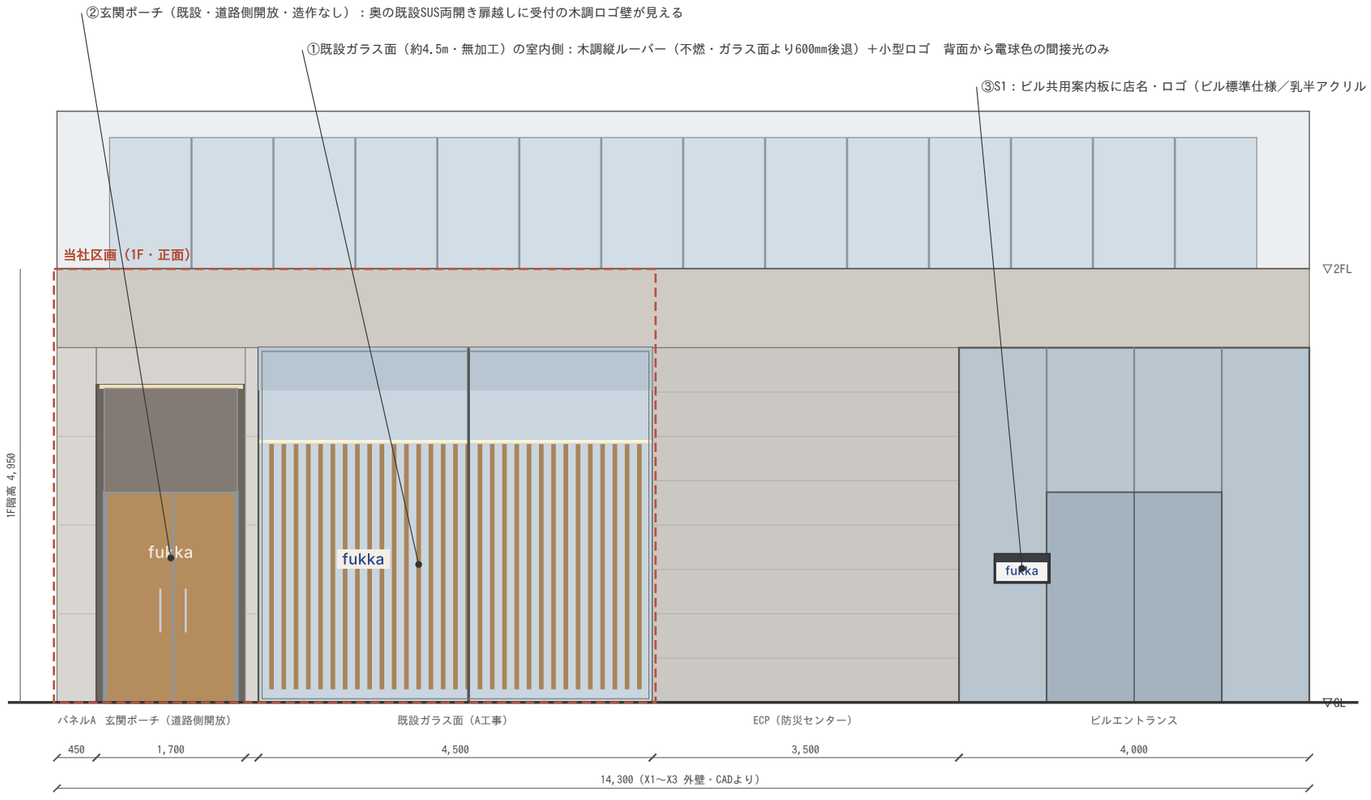

1階 正面部分立面図（サイン位置・使用素材）

S=1/70

サイン詳細（ビル指定仕様に準拠）



S1　W640×H340

ビル共用案内板（エントランス）
乳半アクリル＋ロゴ出力・LED内照
表示：ロゴのみ／約0.14㎡



S2　W300×H300

X1通り側・ビル指定位置
マットアクリル＋ダイノック
白切文字／約0.09㎡

外装サイン方針

（貸主ご意向：落ち着いた外観）


- 突出・袖看板、壁面大型看板は設けない
- ガラス面のフィルム・ポスター広告なし
- S1・S2以外の屋外サインなし
- 点滅・映像・赤色光・ネオン不使用
- 店名・ロゴのみ（価格・施術内容の広告なし）
- 電球色2700〜3000Kの間接光、調光・タイマー
- ガラス面から600mm以上離隔、既設サッシ無加工
- 玄関ポーチは既設のまま（造作・看板なし）
- 表示面積 合計約0.35㎡（上限10㎡）
- 4・5F窓：防炎ロールスクリーンのみ

・1F階高4,950は貸主CAD（展開図 1FL→2FL）より。基準階階高3,900、2F以上の外装は完成予想CGからの模式表現。
・サイン位置・形状はビル側指定（内装マニュアル7-(6)）に準拠。最終仕様は運営管理者と協議のうえ承認を得る。
・正面の当社区画は玄関ポーチ（道路側開放）と既設ガラス面 約4.5mを含む約6.8m（1階 98.36㎡区画・CADより）。ガラス面・サッシは無加工、フィルム等は貼らない。


整形外科ふっか／整痛院ふっか 東京駅院 出店計画 ／ 日本橋WASAMIビル	
外観立面図・サイン計画図 基本計画（出店企画書添付資料）　2026.10	S=1/300・1/70 No.A-04　A3

1F 玄関ポーチ・道路側ガラス面 詳細図


平面詳細　S=1/40

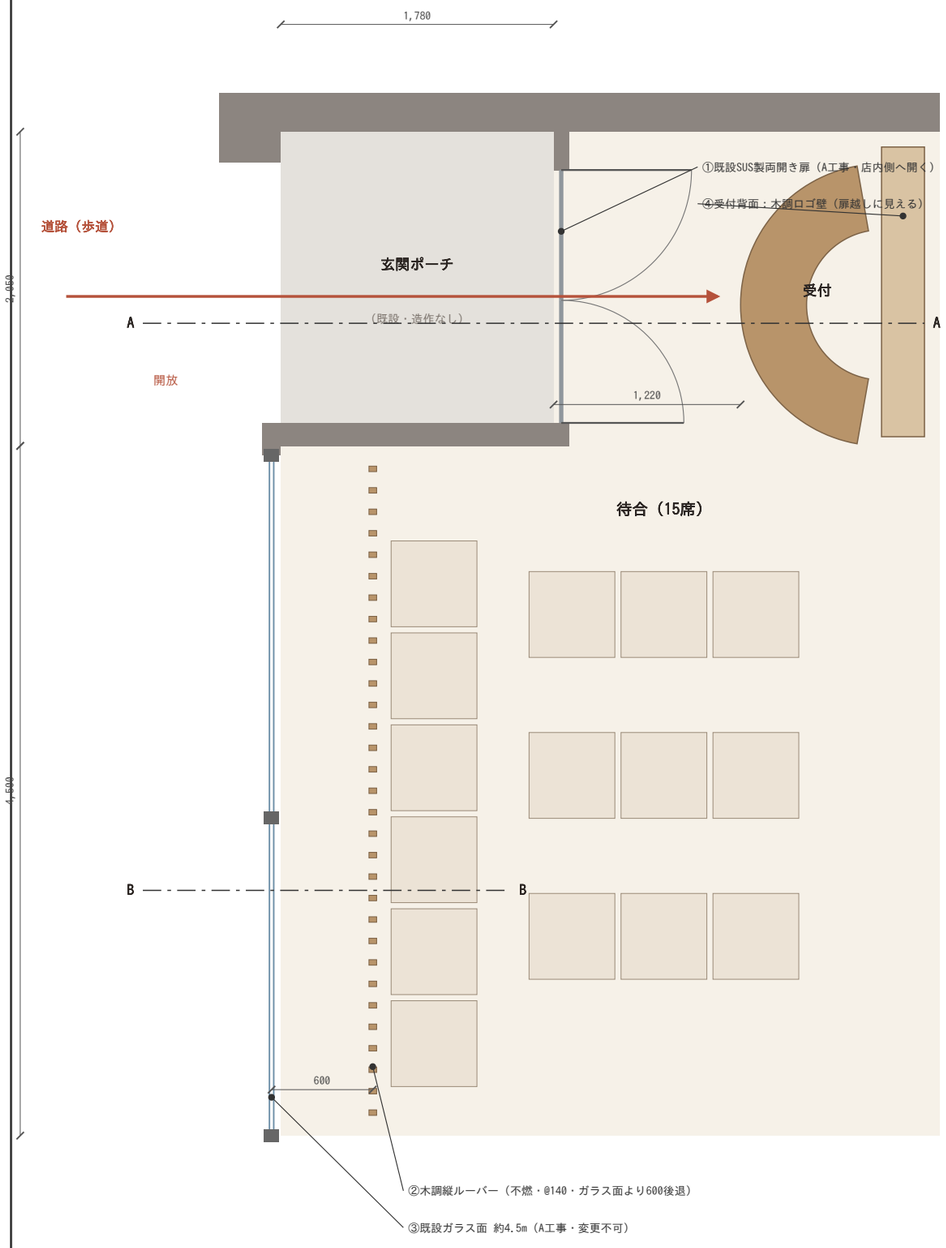


断面 A-A（玄関ポーチ）S=1/50

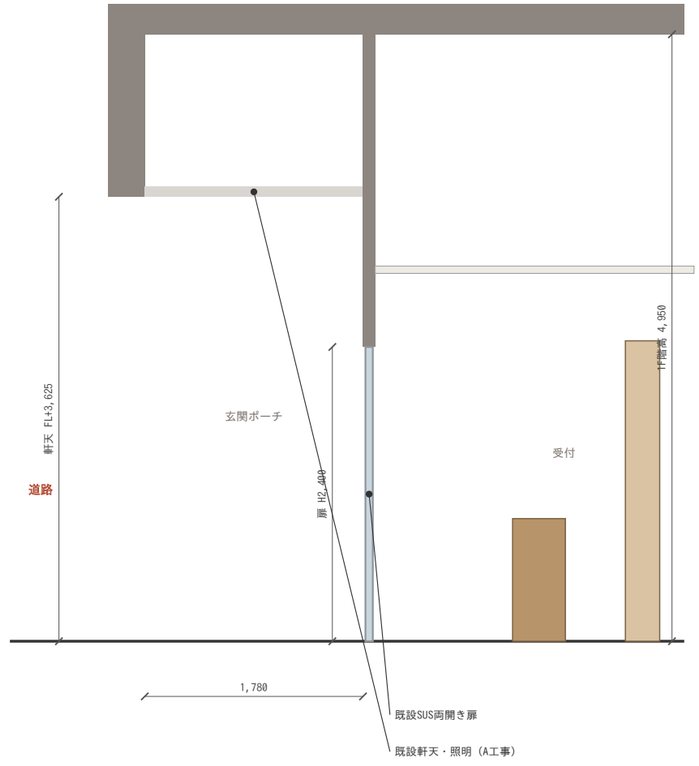

断面 B-B（道路側ガラス面）S=1/50

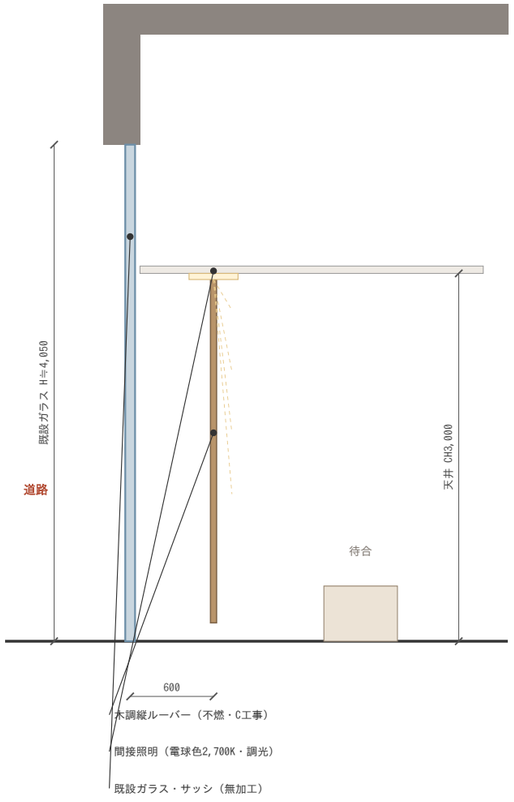

正面（道路から見た当社区画）S=1/80

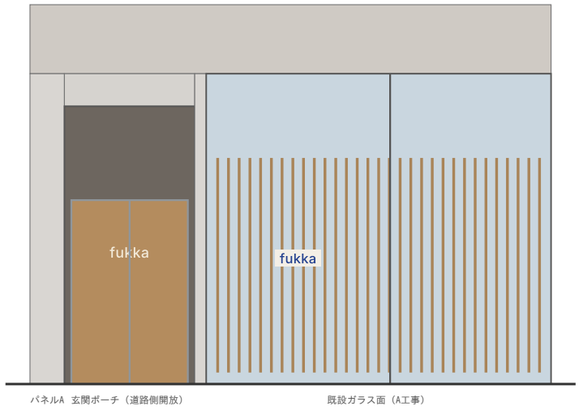

ポーチ奥：既設SUS扉越しに受付の木調ロゴ壁
ガラス面：600mm奥の木調縦ルーバー＋小型ロゴ
看板・ガラス面への貼物なし
→ 立面図 A-04・外装イメージ P.8 と同一

・玄関ポーチは区画内（道路側開放・扉なし）。床・壁・軒天・奥の両開き扉（SUS製）は既設（A工事）のまま使用し、ポーチ内に造作・看板は設けない。
・道路側ガラス面（約4.5m）・サッシは既設（A工事）で変更不可。室内側にガラス面から600mm後退した木調縦ルーバー（不燃・C工事）を設け、外からの視線をやわらげる。
・受付カウンターは扉の内側1,220mmを空けて配置（扉は店内側へ開く）。ロゴは受付背面の木調壁に表示し、扉越しに見える控えめな表示とする。
・寸法は1F CAD（貸主）からの読取り値。ポーチ床の段差・勾配（FL-70〜±0・スロープ1/26）、軒天高さ（FL+3,625）は既設図による。実施設計時に確定。

整形外科ふっか／整痛院ふっか 東京駅院 出店計画 ／ 日本橋WASAMIビル

1F 玄関ポーチ・道路側ガラス面 詳細図

基本計画（出店企画書添付資料）　2026.10

S=1/40・1/50

No.A-05　A3