
← 正面道路（Y1通り・歩道）

1階 平面計画図（玄関ポーチ・受付待合・診察室・処置室・MRI室）

貸室面積 98.36㎡（約29.75坪）

図の向き
左：正面道路（Y1側）
上：X1通り側　※真北は要確認

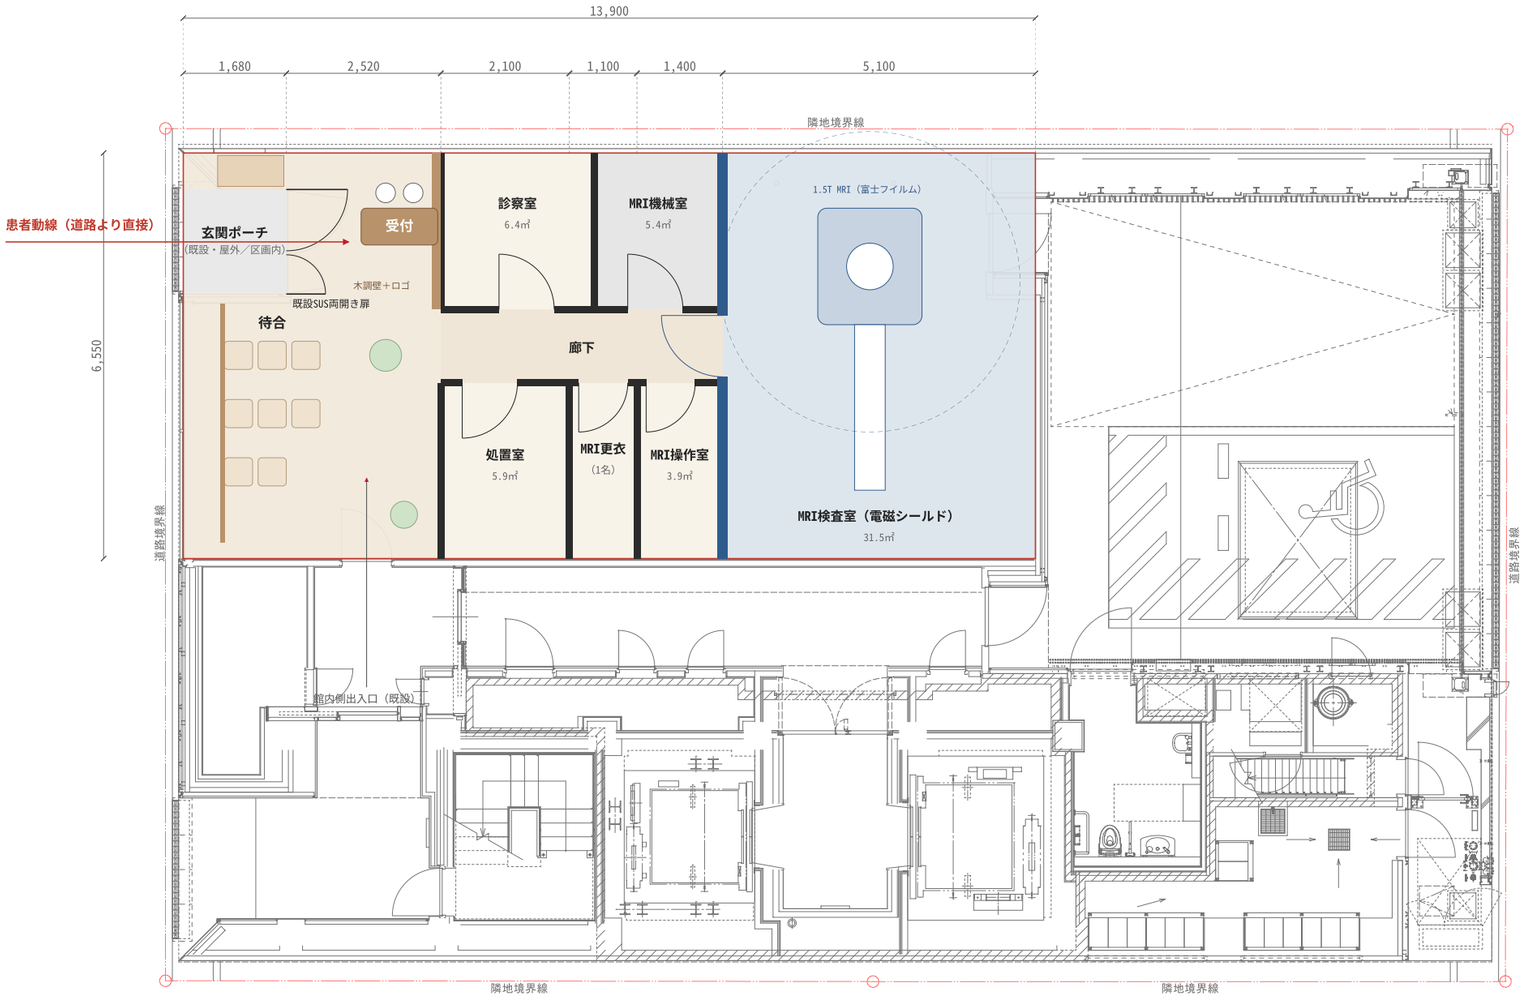

- 貸室 98.36㎡（約29.75坪）
- 診察・処置・操作・更衣
- MRI室（シールド工事）
- 機械室
- 玄関ポーチ（既設・区画内）

諸室面積表（内法・概算）

玄関ポーチ（屋外）	2.9㎡
診察室	6.4㎡
MRI機械室	5.4㎡
処置室	5.9㎡
MRI更衣（1名）	3.1㎡
MRI操作室	3.9㎡
MRI検査室（電磁シールド）	31.5㎡

・下図（グレー）は貸主提供の募集図面（1階 店舗区画）。赤線＝貸室区画（98.36㎡）、着色部・室配置が当社計画（C工事）。
・入口は既設の玄関ポーチ（道路側は開放）と既設SUS製両開き扉（A工事・無加工）の1か所。風除室は設けない。
・扉は店内側に開くため、扉の内側1,220㎜は何も置かない。正面の木調壁にロゴ、受付は扉から見える位置に置く。
・MRI：富士フイルム製1.5T（ゼロヘリウム型想定）。床荷重5,000N/㎡の1Fに配置。搬入経路・振動・電源容量はビル側と協議。
・道路側ガラス面から600㎜以内には造作・サインを設けない（内装マニュアル）。トイレは館内共用トイレを利用。


整形外科ふっか／整痛院ふっか 東京駅院 出店計画 ／ 日本橋WASAMIビル

1階 平面計画図（受付待合・診察室・処置室・MRI室）

基本計画（出店企画書添付資料） 2026.10 改訂（1階 玄関）


S=1/100

No.A-01 A3

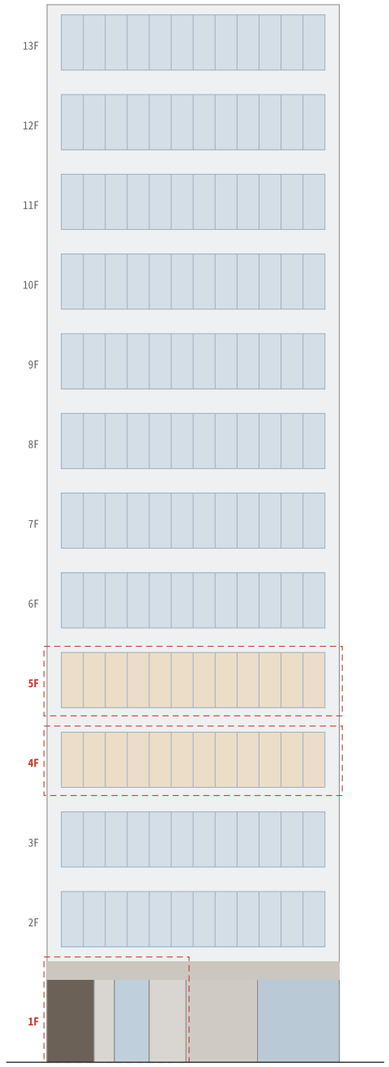

正面全体立面（Y1通り・模式）

S=1/300　赤破線＝当社区画

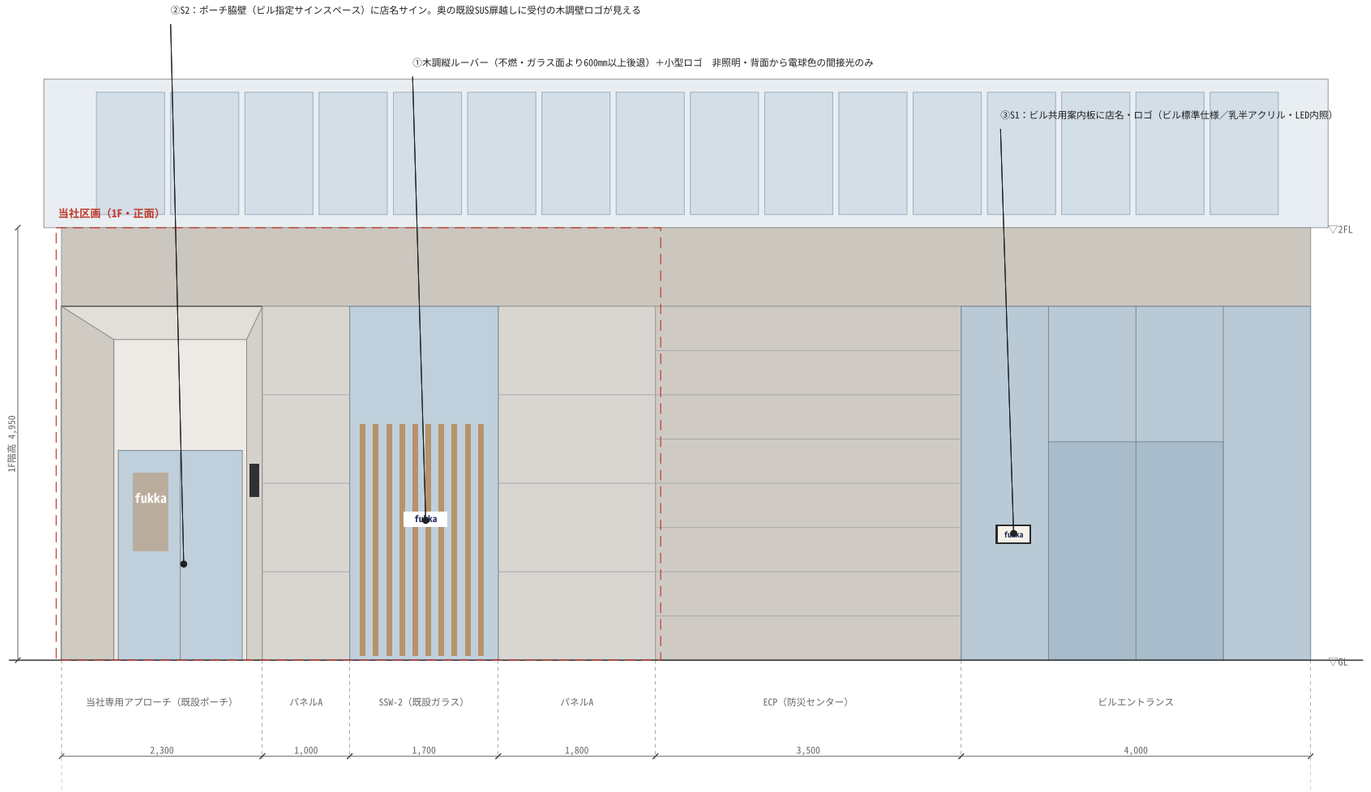

1階 正面部分立面図（サイン位置・使用素材）

S=1/70

サイン詳細（ビル指定仕様に準拠）



S1　W640×H340
ビル共用案内板（エントランス）
乳半アクリル＋ロゴ出力・LED内照
表示：ロゴのみ／約0.14㎡



S2　W300×H300
玄関ポーチ脇壁（店舗用サインスペース）
マットアクリル＋ダイノック
白切文字／約0.09㎡　※寸法・位置はビル基準

外装サイン方針

（貸主ご意向：落ち着いた外観）

- 突出・袖看板、壁面大型看板は設けない
- ガラス面のフィルム・ポスター広告なし
- S1・S2以外の屋外サインなし
- 点滅・映像・赤色光・ネオン不使用
- 店名・ロゴのみ（価格・施術内容の広告なし）
- 電球色2700〜3000Kの間接光、調光・タイマー
- ガラス面から600mm以上離隔、既設サッシ無加工
- 玄関ポーチは既設のまま（造作・扉の追加なし）
- 4・5F窓：防炎ロールスクリーンのみ

・1F階高4,950は貸主CAD（展開図 1FL→2FL）より。基準階階高3,900、2F以上の外装は完成予想CGからの模式表現。
・当社専用アプローチは「道路側開放の玄関ポーチ＋奥の既設SUS製両開き扉（A工事）」。風除室・ガラス扉の新設はしない（改訂）。
・サイン位置・形状はビル側指定（内装マニュアル7-(6)）に準拠。最終仕様は運営管理者と協議のうえ承認を得る。

整形外科ふっか／整痛院ふっか 東京駅院 出店計画 ／ 日本橋WASAMIビル

外観立面図・サイン計画図


基本計画（出店企画書添付資料） 2026.10 改訂（1階 玄関）

S=1/300・1/70

No.A-04　A3


1F 専用アプローチ（玄関ポーチ）詳細図

平面詳細　S=1/40

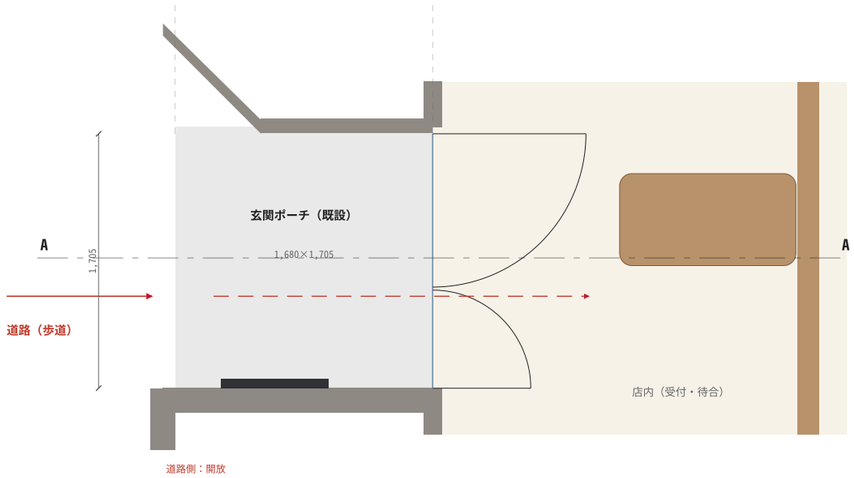


①既設SUS製両開き扉（A工事・無加工）
②S2：ポーチ脇壁サイン（ビル指定サインスペース）
③床・軒天・壁：既設のまま（造作・扉の追加なし）
④店内正面：木調壁＋店名ロゴ（扉越しに見える）

断面詳細 A-A　S=1/40

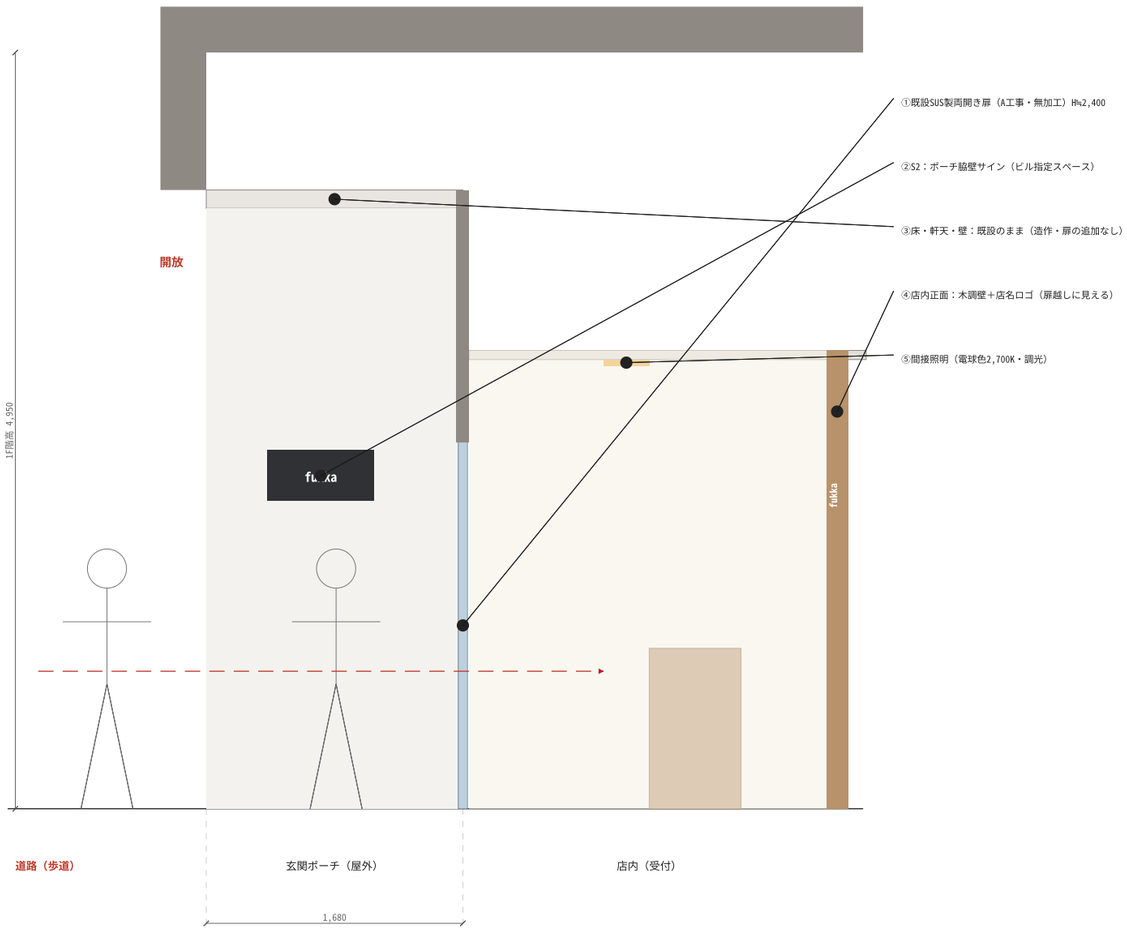

正面（道路から見た姿）S=1/60

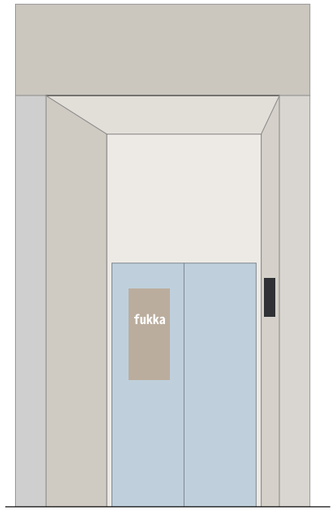

手前：開放（扉なし）
奥：既設SUS扉＋店内の木調壁ロゴ
→ 外装イメージ（P.8）と同一

・既設アプローチ（玄関ポーチ）は区画内。道路側は開放で、扉は奥の既設SUS製両開き扉（A工事）1か所のみ。扉・サッシは無加工。
・当社工事（C工事）は店内側のみ：正面の木調壁＋店名ロゴ、受付カウンター、天井・間接照明。ポーチ内には造作を設けない。
・S2サインはビル指定の店舗用サインスペース（店舗入口脇壁面・屋外）に掲出。寸法・表示はビル基準で事前協議。
・床・軒天は既設仕上げのまま使用。扉高さ・軒天高さ・ポーチ照明の有無は実施設計時に確認（寸法は貸主図面からの読み取り値）。

整形外科ふっか／整痛院ふっか 東京駅院 出店計画 ／ 日本橋WASAMIビル

1F専用アプローチ 詳細図（平面・断面・正面）

基本計画（出店企画書添付資料） 2026.10 改訂（1階 玄関）

S=1/40・1/60

No.A-05 A3

外装イメージ EXTERIOR IMAGE



外装 **正面（Y1通り）外観イメージ**

ビル既設の外装はそのまま。当社の表示は、玄関ポーチ脇壁のS2サイン、SSW-2ガラス奥（600mm後退）の木調ルーバー上の小型ロゴ、ビル共用案内板（S1）のみ。突出看板・ガラス面広告はありません（立面図 A-04 と同一仕様）。



外装 **1F 専用アプローチ（玄関ポーチ）まわり**

道路側は開放のまま。ポーチ奥の既設SUS扉越しに、店内正面の木調壁と店名ロゴが見えます。電球色のダウンライトで、夜も落ち着いた表情です。



正面全景

4・5F窓面は内側の防炎ロールスクリーンのみで、サイン表示はありません。

内装イメージ（1F 入口・受付） INTERIOR IMAGE



内装 **待合から受付を見る**

既設扉（左の壁の奥）から入るとすぐ、正面の木調壁と店名ロゴ、受付カウンターが見えます。扉の内側1,220㎜は何も置かず、車いすでもそのまま受付に着けます。

主な仕上げ

正面壁	木目調不燃化粧板（縦ルーバー）＋店名ロゴ
受付	木調カウンター H1,050／天板 人工大理石
床	タイルカーペット（防炎）／入口1.2mは長尺シート
壁	EP（アイボリー）
天井	PB t9.5+12.5 EP（白）CH3,000
照明	電球色2,700K・調光（間接照明＋ダウンライト）

銀座院と同じ「木調×アイボリー」。内装材はすべて不燃材、カーペットは防炎品。