


STORE OPENING PROPOSAL

# 出店企画書
# 添付資料

## fukka

日本橋院（仮称）

---

物件：日本橋WASAMIビル（東京都中央区日本橋三丁目）

計画区画：1階 店舗区画（約99.7㎡）

4階・5階（募集面積 G229.86㎡）

内容：平面計画図・立面図・サイン計画・外観／内観イメージ・仕上表

2026年10月　基本計画

# 計画概要 PLAN OVERVIEW

| 3 | 19 | 1 |
|---|---|---|
| フロア（1F・4F・5F） | 施術室（4F 9室＋5F 10室） | MRI室（1F） |

## コンセプト

銀座院の空間（白い塗り壁、木目、ベージュ系カーペット、中央の円形受付と木の天井リング）をそのまま拡大し、 施術ブースを増やした「銀座院の大型版」として計画します。1階は道路から直接入れる既設アプローチを活かした医療フロア（診察・処置・MRI）、 4階は受付・待合・更衣と施術室、5階は施術室とフリースペース・スタッフエリアとしています。

## フロア構成

| | |
|---|---|
| 1F | 診察室、処置室、MRI操作室、MRI機械室、MRI室（磁気シールド）、待合 |
| 4F | 施術室 9室、更衣室（男性）、更衣室（女性）、パウダーコーナー、カウンセリング室、待合、スタッフステーション、物品・リネン庫 |
| 5F | 施術室 10室、スタッフ休憩室、スタッフ更衣室、フリースペース、リネン・洗濯室、事務室、物品庫 |

## 動線

新規・検査の患者：道路 → 1F専用アプローチ → 受付 → 診察・MRI
施術の利用者：ビルEV → 4F受付 → 更衣室 → 4F／5F施術室（EV移動）
スタッフ：5F休憩室・更衣室・事務室を拠点に各階へ




4F 4F 俯瞰（受付・待合・更衣・施術室）




5F 5F 俯瞰



1F 1F 俯瞰

# 1階 平面計画図（診察・処置・MRI・受付待合）

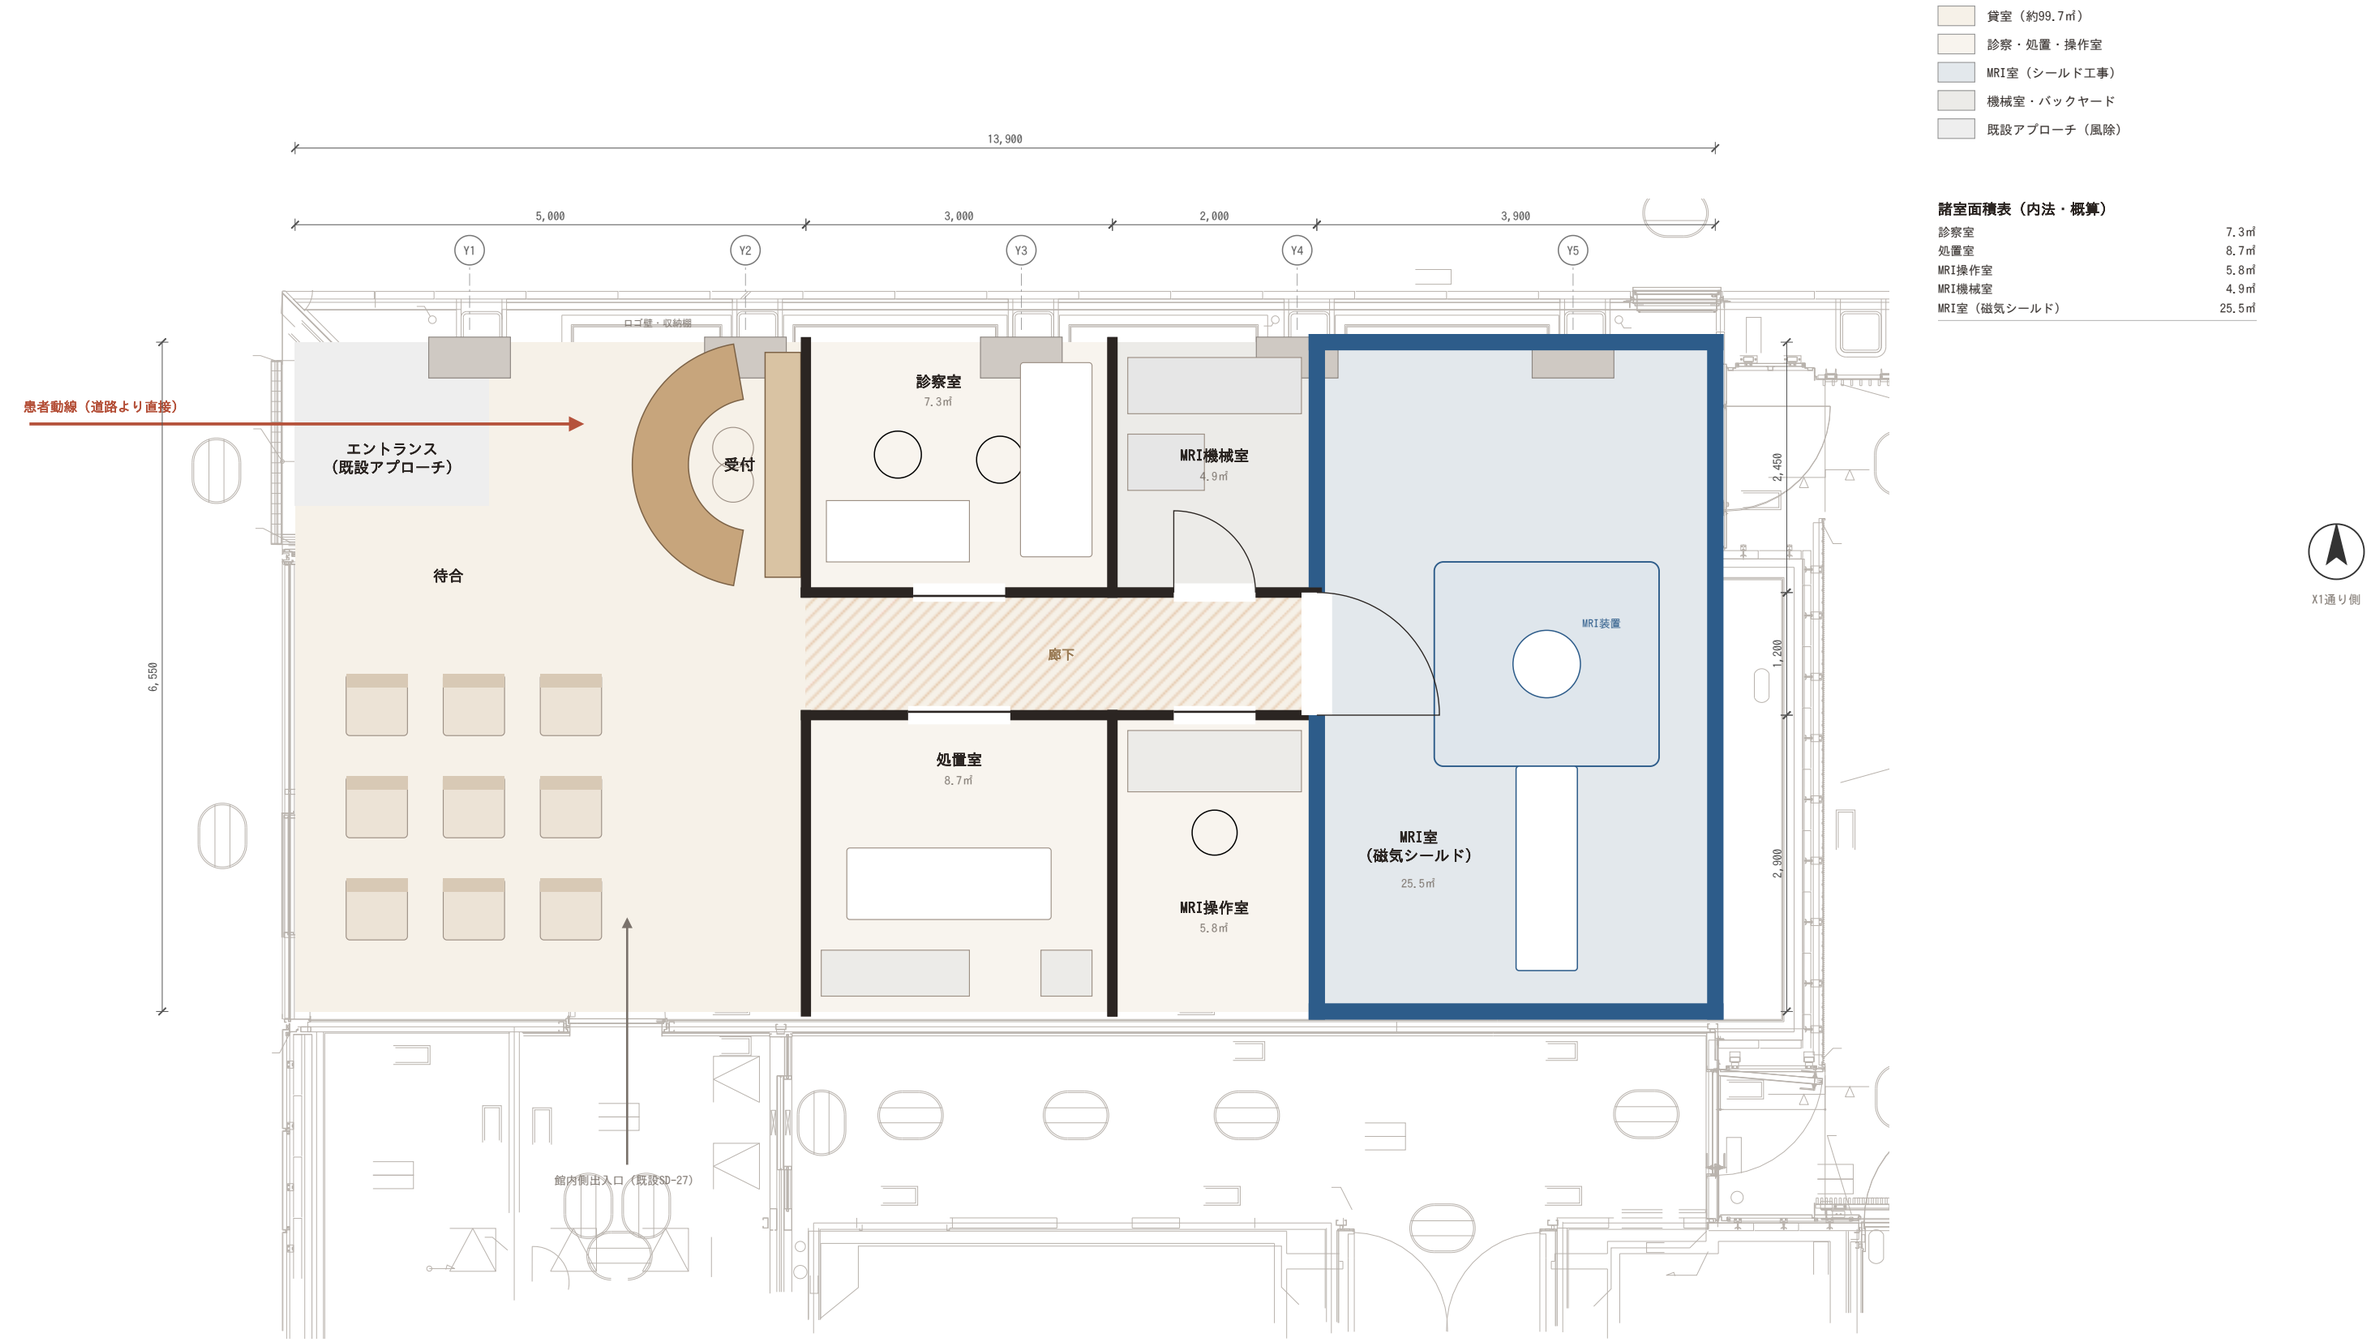


**諸室面積表（内法・概算）**

| | |
|---|---|
| 診察室 | 7.3㎡ |
| 処置室 | 8.7㎡ |
| MRI操作室 | 5.8㎡ |
| MRI機械室 | 4.9㎡ |
| MRI室（磁気シールド） | 25.5㎡ |

・既存建物線（グレー）は貸主提供CAD（1階総合図）より。赤字の動線・室配置が当社計画（C工事）。
・MRIは床荷重5,000N/㎡（1〜3F設定）の1階に配置。機種決定後に重量・磁場・シールド・搬入経路をビル側と協議。
・道路側ガラス面から600mm以内には造作・サインを設けない（内装マニュアル7-(7)）。
・トイレは館内共用トイレ（1F HCWC含む）を利用。間仕切・内装材は全て不燃材、カーペットは防炎品。

| | |
|---|---|
| fukka 日本橋院（仮称） 出店計画 ／ 日本橋WASAMIビル | |
| 1階 平面計画図（診察・処置・MRI・受付待合）<br>基本計画（出店企画書添付資料） 2026.10 | S=1/60<br>No.A-01 A3 |

# 4階 平面計画図（受付・待合・更衣室・施術室）

← 正面道路（Y1通り）




X1通り側

- 施術室（銀座院仕様）
- 個室（更衣・カウンセリング等）
- バックヤード
- 避難経路（廊下状）
- 共用部（コア）

**諸室面積表（内法・概算）**

| | |
|---|---|
| 施術室 × 9室 | 各6.4〜6.4㎡ |
| 更衣室（男性） | 6.4㎡ |
| 更衣室（女性） | 7.3㎡ |
| カウンセリング室 | 9.6㎡ |
| スタッフステーション | 13.2㎡ |
| 物品・リネン庫 | 13.2㎡ |

※コア形状は1階CAD・募集図面からの想定。実寸はビル側図面にて要確認

・施術室 4F 9室 ＋ 5F 10室 ＝ 計19室（要件15〜20室）。間仕切は上部開放の棚間式（棚間h=500）とし防災設備を大部屋仕様のまま活用。
・受付は銀座院と同様にフロア中央へ配置。EVホール〜避難階段附室の経路は廊下状に整備（内装マニュアル6-(7)）。
・EVホール入口の防火扉の開閉を妨げる造作・什器は設けない。床荷重3,000N/㎡内で計画。
・平面寸法は募集図面（G229.86㎡）・1F CADからの想定値。実施設計時にビル側白図で確定。

| | |
|---|---|
| fukka 日本橋院（仮称） 出店計画 ／ 日本橋WASAMIビル | |
| 4階 平面計画図（受付・待合・更衣室・施術室）<br>基本計画（出店企画書添付資料） 2026.10 | S=1/85<br>No.A-02 A3 |

# 5階 平面計画図（施術室・フリースペース・スタッフ休憩室）

← 正面道路（Y1通り）




※コア形状は1階CAD・募集図面からの想定。実寸はビル側図面にて要確認

X1通り側

- 施術室（銀座院仕様）
- 個室（更衣・カウンセリング等）
- バックヤード
- 避難経路（廊下状）
- 共用部（コア）

**諸室面積表（内法・概算）**

| | |
|---|---|
| 施術室 × 10室 | 各6.4〜6.8㎡ |
| スタッフ休憩室 | 22.3㎡ |
| スタッフ更衣室 | 9.6㎡ |
| リネン・洗濯室 | 6.0㎡ |
| 事務室 | 13.2㎡ |
| 物品庫 | 10.8㎡ |


・施術室 10室、フリースペース、スタッフ休憩室・スタッフ更衣室・事務室を配置。
・フリースペースは施術前後の待合・カウンセリング・セミナー兼用のラウンジとして計画。
・EVホール〜避難階段附室の経路は廊下状に整備（4Fと同一）。窓側は施術室の自然光を確保。
・平面寸法は募集図面・1F CADからの想定値。実施設計時にビル側白図で確定。

fukka 日本橋院（仮称） 出店計画 ／ 日本橋WASAMIビル

5階 平面計画図（施術室・フリースペース・スタッフ休憩室） S=1/85


基本計画（出店企画書添付資料） 2026.10 No.A-03 A3

# 外観立面図・サイン計画図（正面 Y1通り）

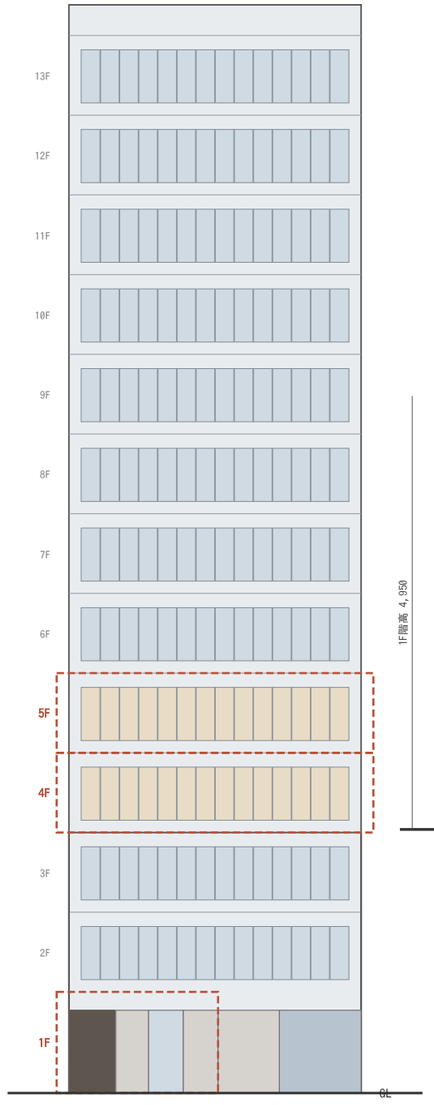


正面全体立面（Y1通り・模式）

S=1/300　赤破線＝当社区画

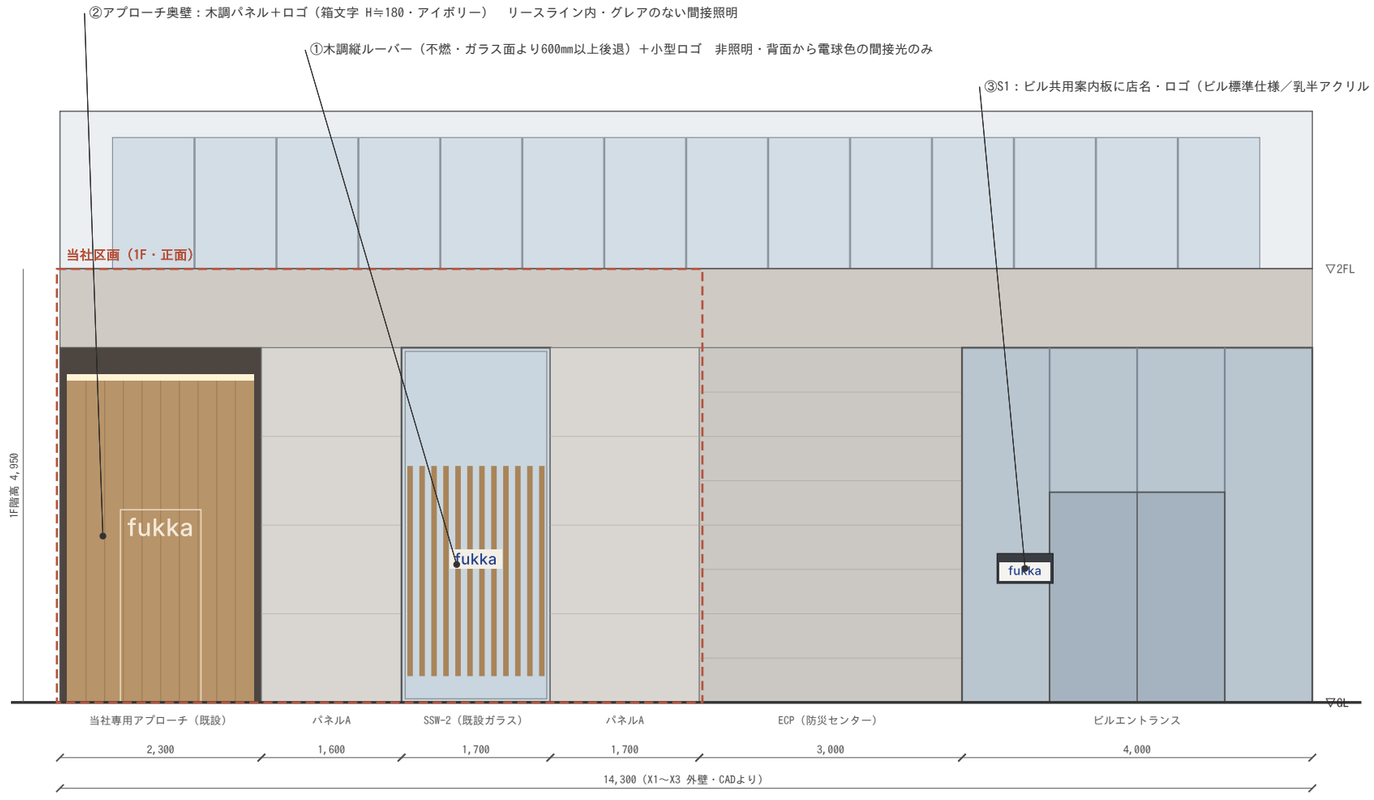


1階 正面部分立面図（サイン位置・使用素材）

S=1/70

## サイン詳細（ビル指定仕様に準拠）




**S1　W640×H340**

ビル共用案内板（エントランス）
乳半アクリル＋ロゴ出力・LED内照
表示：ロゴのみ／約0.14㎡




**S2　W300×H300**

X1通り側・ビル指定位置
マットアクリル＋ダイノック
白切文字／約0.09㎡

## 外装サイン方針


（貸主ご意向：落ち着いた外観）

- 突出・袖看板、壁面大型看板は設けない
- ガラス面のフィルム・ポスター広告なし
- S1・S2以外の屋外サインなし
- 点滅・映像・赤色光・ネオン不使用
- 店名・ロゴのみ（価格・施術内容の広告なし）
- 電球色2700～3000Kの間接光、調光・タイマー
- ガラス面から600㎜以上離隔、既設サッシ無加工
- 表示面積 合計約0.35㎡（上限10㎡）
- 4・5F窓：防炎ロールスクリーンのみ

・1F階高4,950は貸主CAD（展開図 1FL→2FL）より。基準階階高3,900、2F以上の外装は完成予想CGからの模式表現。
・サイン位置・形状はビル側指定（内装マニュアル7-(6)）に準拠。最終仕様は運営管理者と協議のうえ承認を得る。
・正面の当社区画は既設アプローチ・SSW-2ガラス面を含む約7.3m。ガラス面への熱割れ計算が必要なフィルム等は使用しない。

| | |
|---|---|
| fukka 日本橋院（仮称） 出店計画 ／ 日本橋WASAMIビル | |
| 外観立面図・サイン計画図<br>基本計画（出店企画書添付資料）　2026.10 | S=1/300・1/70<br>No.A-04　A3 |

# 外装イメージ EXTERIOR IMAGE

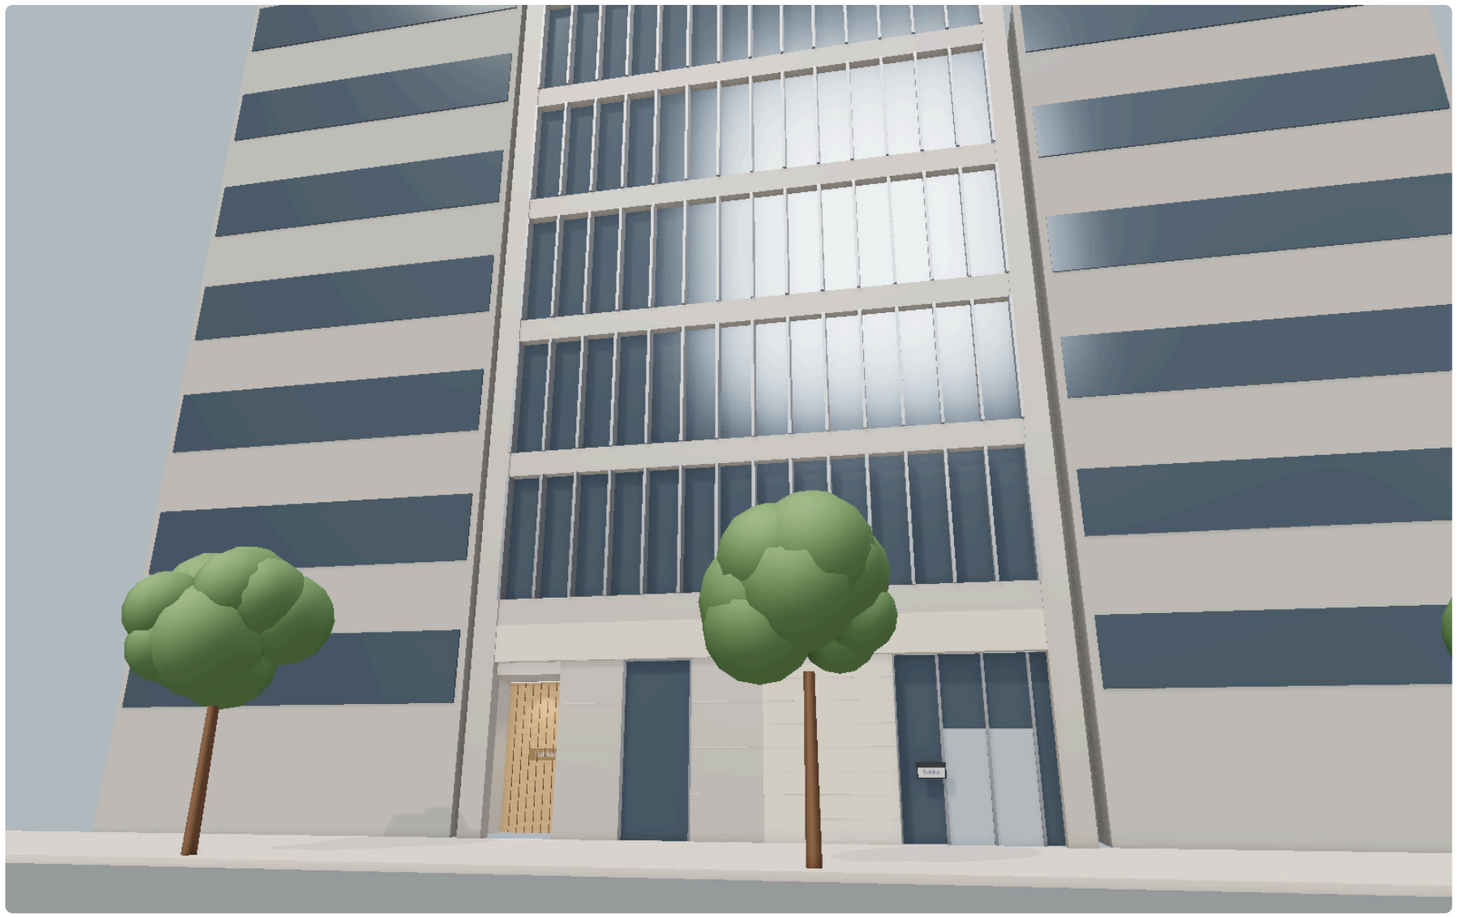

**外装　正面（Y1通り）外観イメージ**

既設の外装はそのまま、当社の表示は1F専用アプローチ奥の木調壁ロゴ、SSW-2ガラス奥の木調ルーバー、ビル共用案内板（S1）のみ。突出看板・ガラス面広告は設けません。




**外装　1F 専用アプローチまわり**

木調パネル＋アイボリーのロゴ（リースライン内）。照明は電球色の間接光のみで、夜間もまぶしさが出ない計画です。

**サイン表示（合計 約0.35㎡）**


S1 ビル案内板：ロゴのみ／S2 ビル指定位置：W300角プレート／1F窓：600mm後退ルーバー上の小型ロゴ（非照明）／4・5F窓：表示なし（ロールスクリーンのみ）

# 内装イメージ　1階（診察・処置・MRI・受付待合）　INTERIOR IMAGE 1F




1F **1F 受付・待合**

道路側アプローチから入ると正面に円形受付。銀座院と同じ木の天井リングと木目のロゴ壁。道路側ガラス面の内側は600mm後退した木調ルーバーで外からの視線をやわらげます。

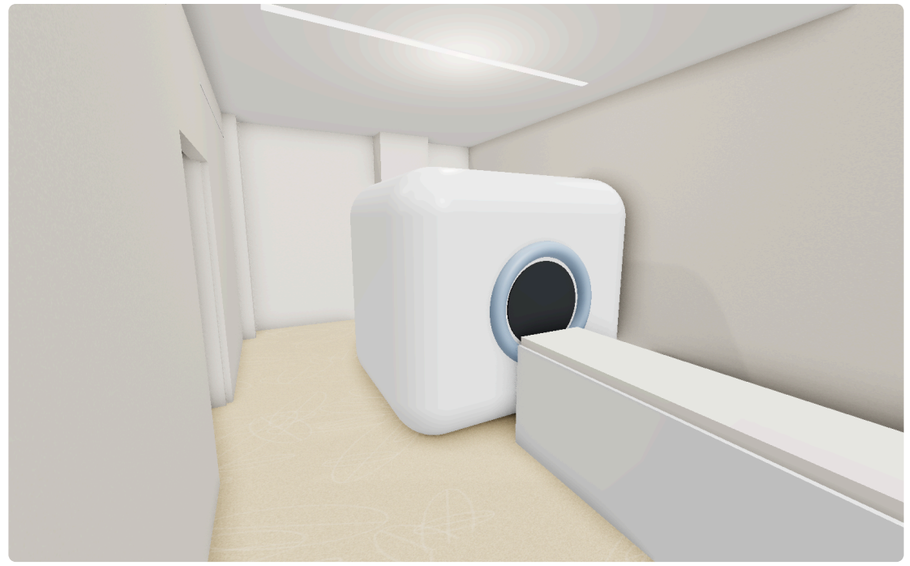

1F **MRI室**

磁気シールド工事を行う独立区画。操作室から観察窓で確認。



1F **1F 俯瞰**

受付待合／診察・処置／MRI（操作室・機械室）

# 内装イメージ　4階（受付・待合・更衣室・施術室）

INTERIOR IMAGE 4F




**4F　4F 受付・待合（フロア中央の受付）**

EVホールから自動ドアを入ると正面に受付。銀座院と同じ円形カウンター、木の天井リング、棚とロゴ壁の構成を拡大して再現しています。



**4F　施術室前の通路**

窓側に施術室を並べ、木目の引戸と白い壁で統一。



**4F　施術室（約6.4㎡）**

ベッド・スツール・荷物かご・棚。窓側で自然光を確保。

# 内装イメージ　5階（施術室・フリースペース・スタッフ休憩室）

INTERIOR IMAGE 5F



5F **5F フリースペース**

施術前後の待合、カウンセリング、小規模セミナーに使えるラウンジ。造作ベンチと丸テーブルで、銀座院と同じ素材・色を使います。



5F **5F 俯瞰**

施術室10室／フリースペース／スタッフ休憩室・更衣室・事務室




参考 **参考：銀座院（既存）**

トーン＆マナーはこの内装を基準にしています。

# 仕上表・ビル規定への対応 FINISH SCHEDULE / COMPLIANCE

## 仕上表（概略・基本計画段階）

| 部位 | 仕上 | 備考 |
|---|---|---|
| 床 | タイルカーペット（防炎品・ベージュ系、銀座院同等柄）／MRI室・処置室：ビニル床シート | OAフロア（4・5F）上に施工 |
| 巾木 | ソフト巾木 H60（ベージュ） | |
| 壁 | LGS＋PB12.5（不燃）下地　AEP塗装（白・塗り壁調）／受付背面：木目調不燃化粧板 | 施術室間仕切は上部開放の欄間式（欄間 h=500） |
| 天井 | 既設天井（4・5F CH2,800）／1F：PB下地 AEP（CH約3,000）　受付上部：木目調リング（不燃） | 既設防災設備（感知器・SP・非常照明）を活かす |
| 建具 | 施術室：木目調不燃化粧板 引戸 W900×H2,100／エントランス：ガラス自動ドア | 鍵1本をビル側へお預け |
| 家具 | 受付カウンター（木目＋白天板）、待合チェア（ベージュ張地・木脚）、施術ベッド | 家具は防炎・難燃材料を優先 |
| 照明 | LEDライン照明・ダウンライト（電球色～温白色 3000～3500K、調光） | ビル電源容量内（1Φ約100VA/㎡、3Φ約200VA/㎡） |
| カーテン等 | 窓：防炎ロールスクリーン（アイボリー） | 防炎ラベル縫付 |
| MRI室 | 磁気シールド・RFシールド工事（専門業者）、専用電源・空調・チラー | 床荷重・搬入経路・振動対策をビル側と協議 |

## 内装マニュアル（ビル規定）への対応

| | |
|---|---|
| 床荷重 | 1F 5,000N/㎡、4・5F 3,000N/㎡。重量物（MRI）は1Fに配置 |
| 間仕切 | 不燃材使用。欄間式とし、防災設備の追加が必要な場合はB工事で対応 |
| 避難経路 | 2～5F：EVホール～避難階段附室を廊下状に整備。防火扉の開閉を妨げる造作なし |
| ファサード | 既設サッシ・ガラスは無加工、ガラス面から600mm以上離隔 |
| サイン | ビル指定場所（S1・S2）のみ。点滅・映像・赤色光・ネオン不使用、店名ロゴのみ |
| 設備 | 空調・電源は基準容量内。給排水（診察室・処置室の手洗い）は区画内の排水位置から計画、必要に応じ防水・漏水検知 |
| 用途 | 誘導用途区画のため診療所・施術所としての適合性を事前確認 |
| 提出図書 | B工事指示書・基本設計図書：着工2.5か月前／実施設計図・工事申請書：着工1か月前 |

※本資料は出店審査用の基本計画です。寸法・面積は募集資料および1F CADからの想定値で、 実施設計時にビル側の白図・設備図に基づき確定します。パースはイメージで、実際の仕上・家具とは異なる場合があります。