

STORE OPENING PROPOSAL

出店企画書
添付資料

fukka

日本橋院（仮称）

物件：日本橋WASAMIビル（東京都中央区日本橋三丁目）

計画区画：1階 店舗区画 98.36㎡（約29.75坪）

4階・5階 各 G229.86㎡（約69.53坪）

合計 約168.8坪

内容：平面計画図・立面図・サイン計画・外観／内観イメージ・仕上表

2026年10月　基本計画

計画概要 PLAN OVERVIEW

168.8坪
1F 29.75坪＋4F・5F 各69.53坪

18
施術室（4F 8室＋5F 10室）

1
MRI室（1F）

コンセプト

銀座院の空間（白い塗り壁、木目、ベージュ系カーペット、中央の円形受付と木の天井リング）をそのまま拡大し、 施術ブースを増やした「銀座院の大型版」として計画します。1階は道路から直接入れる既設アプローチを活かした医療フロア（診察・処置・MRI）、 4階は受付・待合・更衣と施術室、5階は施術室とフリースペース・スタッフエリアとしています。

フロア構成


1F 98.36㎡ 約29.75坪	診察室、処置室、MRI操作室、MRI更衣室、MRI室（磁気シールド）、MRI機械室、待合
4F 229.86㎡ 約69.53坪	施術室 8室、更衣室（男性）、更衣室（女性）、待合、カウンセリング室、物品・リネン庫、スタッフステーション
5F 229.86㎡ 約69.53坪	施術室 10室、リネン庫、スタッフ休憩室、スタッフ更衣（男）、スタッフ更衣（女）、フリースペース、物品庫、事務室

動線

新規・検査の患者：道路 → 1F専用アプローチ → 受付 → 診察・MRI
施術の利用者：ビルEV → 4F受付 → 更衣室 → 4F／5F施術室（EV移動）
スタッフ：5F休憩室・更衣室・事務室を拠点に各階へ



4F 4F 俯瞰（受付・待合・更衣・施術室）

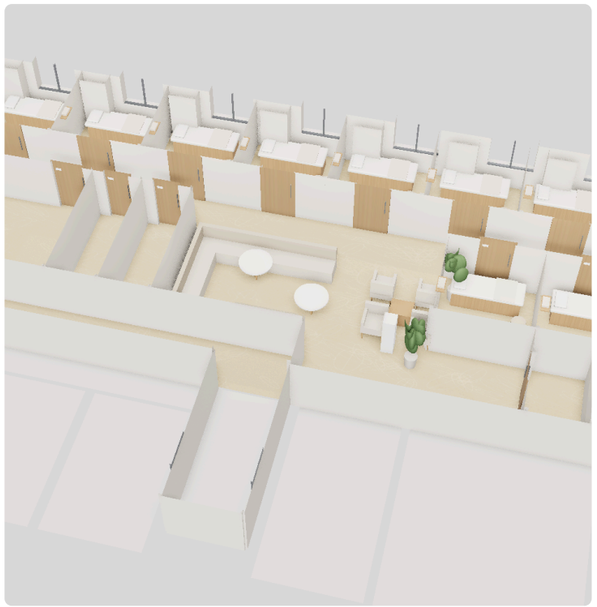

5F 5F 俯瞰




1F 1F 俯瞰

1階 平面計画図（受付待合・診察室・処置室・MRI室）

貸室面積 98.36㎡（約29.75坪）

← 正面道路（Y1通り・歩道）

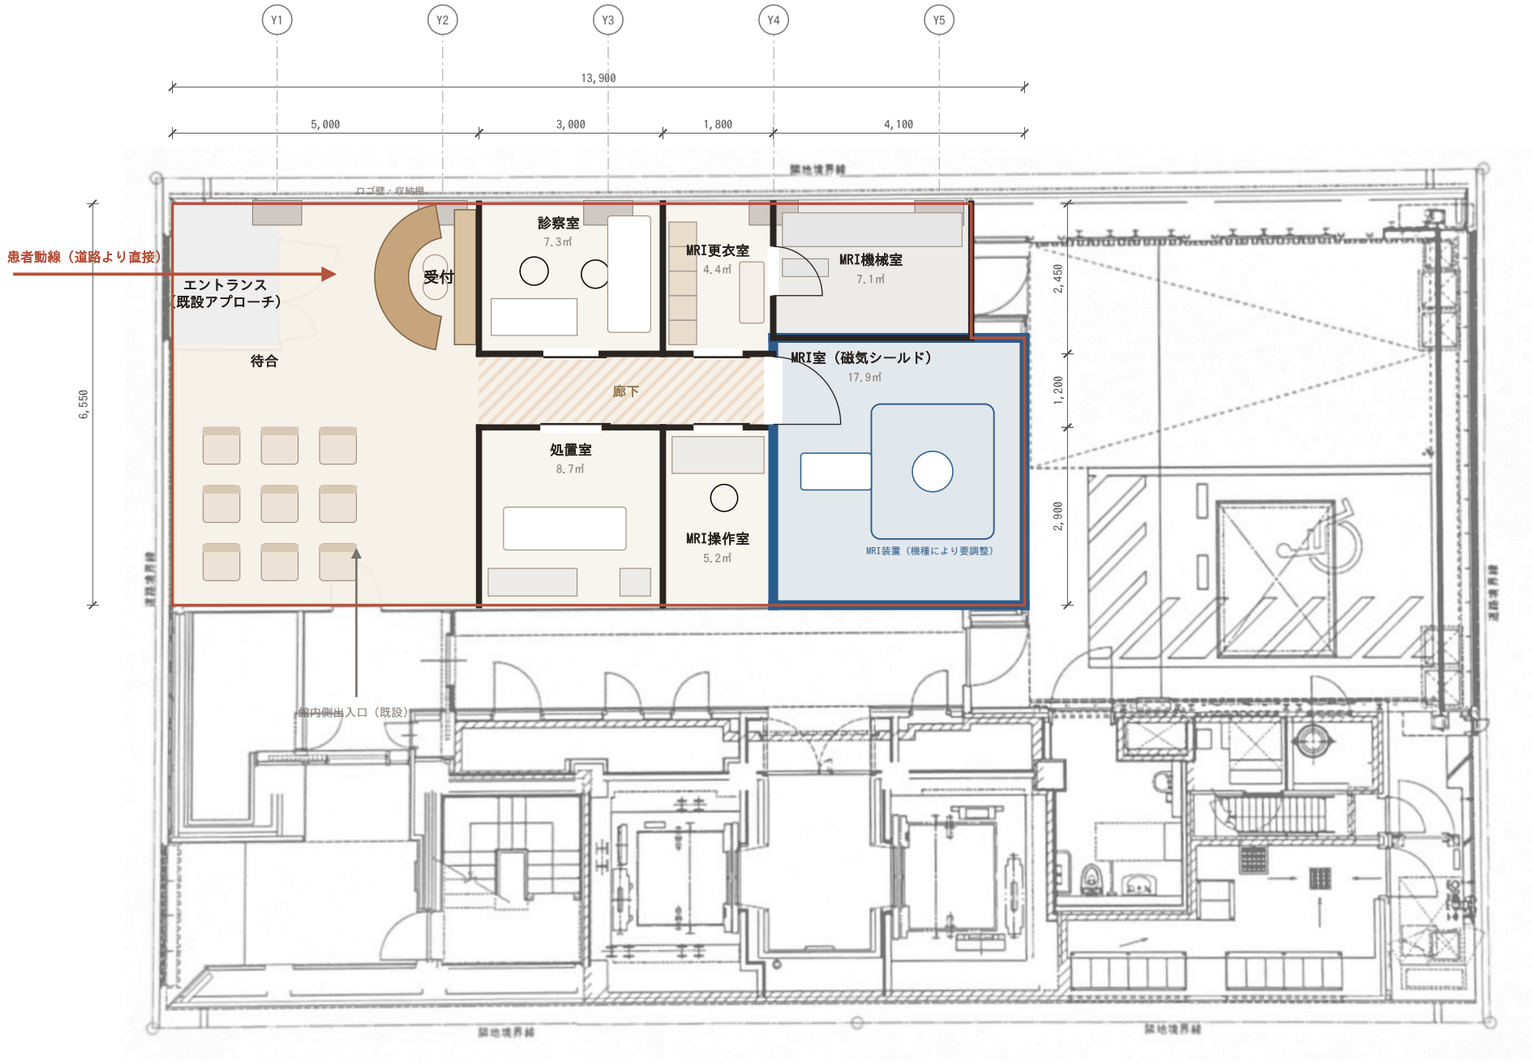

X1通り側

- 貸室 98.36㎡（約29.75坪）
- 診察・処置・操作・更衣
- MRI室（シールド工事）
- 機械室
- 既設アプローチ（区画内）

諸室面積表（内法・概算）

診察室	7.3㎡
処置室	8.7㎡
MRI操作室	5.2㎡
MRI更衣室	4.4㎡
MRI室（磁気シールド）	17.9㎡
MRI機械室	7.1㎡


・下図（グレー）は貸主提供の募集図面（1階 店舗区画）。赤線＝貸室区画（98.36㎡）、着色部・室配置が当社計画（C工事）。
・MRIは床荷重5,000N/㎡（1〜3F設定）の1階に配置。機種決定後に重量・磁場・シールド・搬入経路をビル側と協議。
・道路側ガラス面から600mm以内には造作・サインを設けない（内装マニュアル7-(7)）。
・トイレは館内共用トイレを利用。間仕切・内装材は全て不燃材、カーペットは防炎品。

fukka 日本橋院（仮称） 出店計画 ／ 日本橋WASAMIビル	
1階 平面計画図（受付待合・診察室・処置室・MRI室） 基本計画（出店企画書添付資料） 2026.10	S=1/100 No.A-01 A3

4階 平面計画図（受付・待合・更衣室・施術室）

貸室面積 G229.86㎡（約69.53坪）

← 正面道路（Y1通り）

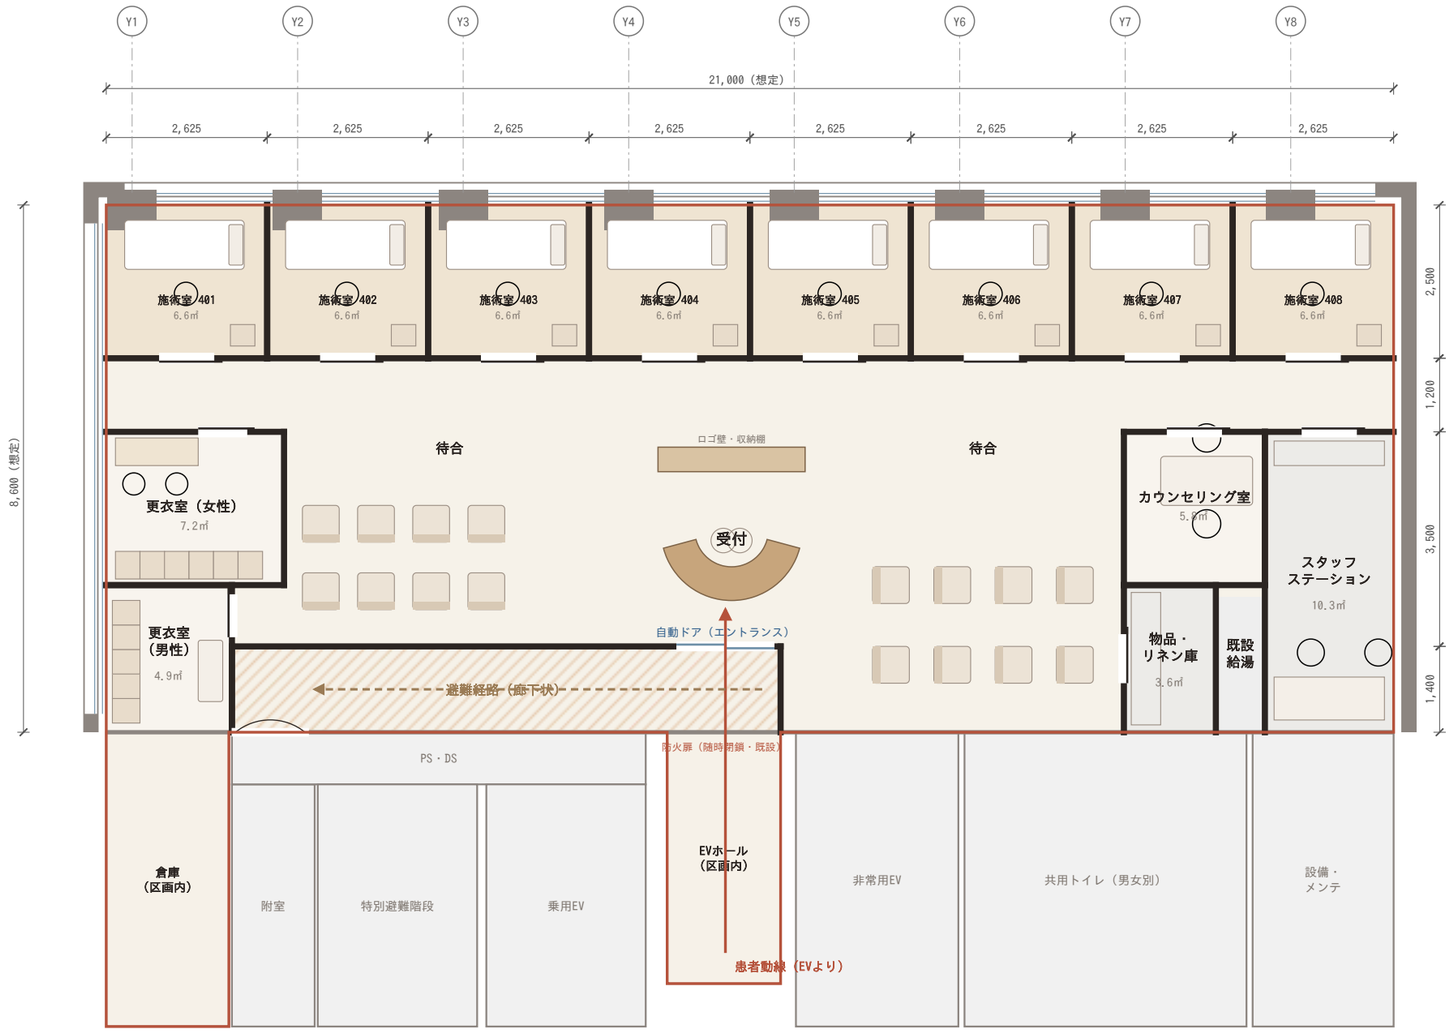

X1通り側

※コアは募集図面（4・5階）をもとに作図。実寸はビル側図面にて要確認

- 貸室 G229.86㎡（約69.53坪）
- 施術室（銀座院仕様）
- 個室（更衣・カウンセリング等）
- バックヤード
- 避難経路（廊下状）
- 共用部（コア）

諸室面積表（内法・概算）

施術室 × 8室	各6.6〜6.6㎡
更衣室（男性）	4.9㎡
更衣室（女性）	7.2㎡
カウンセリング室	5.8㎡
物品・リネン庫	3.6㎡
スタッフステーション	10.3㎡


・施術室 4F 8室 ＋ 5F 10室 ＝ 計18室（要件15〜20室）。間仕切は上部開放の欄間式（欄間h=500）とし防災設備を大部屋仕様のまま活用。
・受付は銀座院と同様にフロア中央へ配置。EVホール（区画内）～避難階段附室の経路は廊下状に整備（内装マニュアル6-(7)）。
・EVホール入口の防火扉の開閉を妨げる造作・什器は設けない。床荷重3,000N/㎡内で計画。
・平面形状は募集図面（4・5階 G229.86㎡）をもとに作図。実施設計時にビル側白図で寸法を確定。

fukka 日本橋院（仮称） 出店計画 ／ 日本橋WASAMIビル	
4階 平面計画図（受付・待合・更衣室・施術室） 基本計画（出店企画書添付資料） 2026.10	**S=1/100** No.A-02 A3

5階 平面計画図（施術室・フリースペース・スタッフ休憩室）

貸室面積 G229.86㎡（約69.53坪）

← 正面道路（Y1通り）

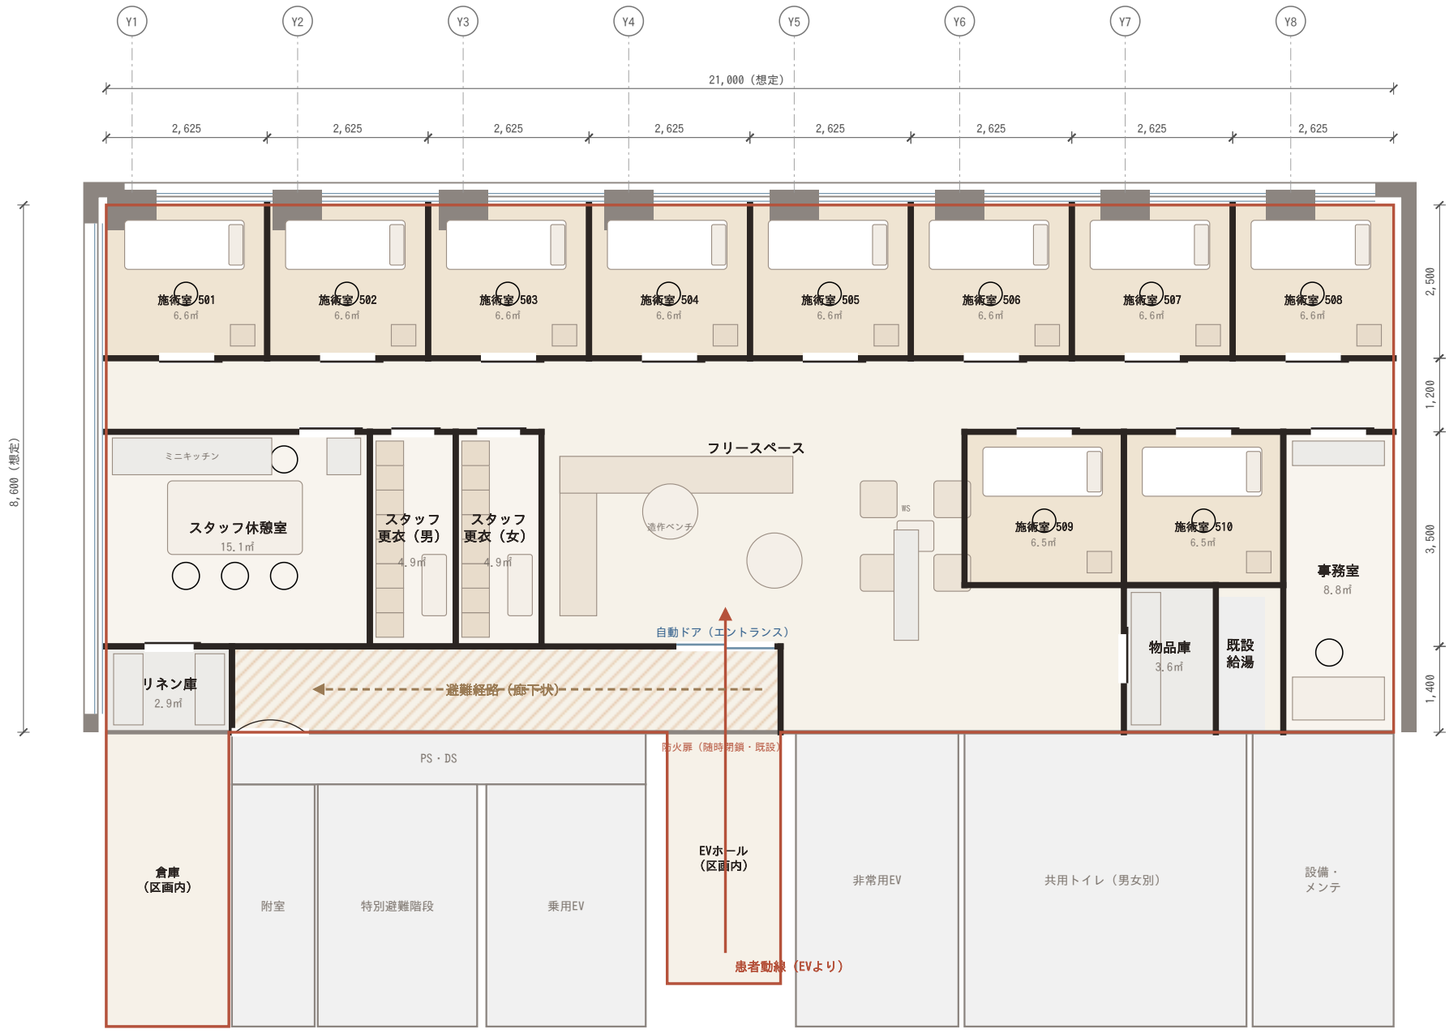

X1通り側

- 貸室 G229.86㎡（約69.53坪）
- 施術室（銀座院仕様）
- 個室（更衣・カウンセリング等）
- バックヤード
- 避難経路（廊下状）
- 共用部（コア）

諸室面積表（内法・概算）


施術室 × 10室	各6.5〜6.6㎡
リネン庫	2.9㎡
スタッフ休憩室	15.1㎡
スタッフ更衣（男）	4.9㎡
スタッフ更衣（女）	4.9㎡
物品庫	3.6㎡
事務室	8.8㎡

※コアは募集図面（4・5階）をもとに作図。実寸はビル側図面にて要確認

・施術室 10室、フリースペース、スタッフ休憩室・スタッフ更衣室（男女）・事務室を配置。
・フリースペースは施術前後の待合・カウンセリング・セミナー兼用のラウンジとして計画。
・EVホール（区画内）～避難階段附室の経路は廊下状に整備（4Fと同一）。窓側は施術室の自然光を確保。
・平面形状は募集図面（4・5階 G229.86㎡）をもとに作図。実施設計時にビル側白図で寸法を確定。


fukka 日本橋院（仮称） 出店計画 ／ 日本橋WASAMIビル	
5階 平面計画図（施術室・フリースペース・スタッフ休憩室）	S=1/100
基本計画（出店企画書添付資料） 2026.10	No.A-03 A3

外観立面図・サイン計画図（正面 Y1通り）

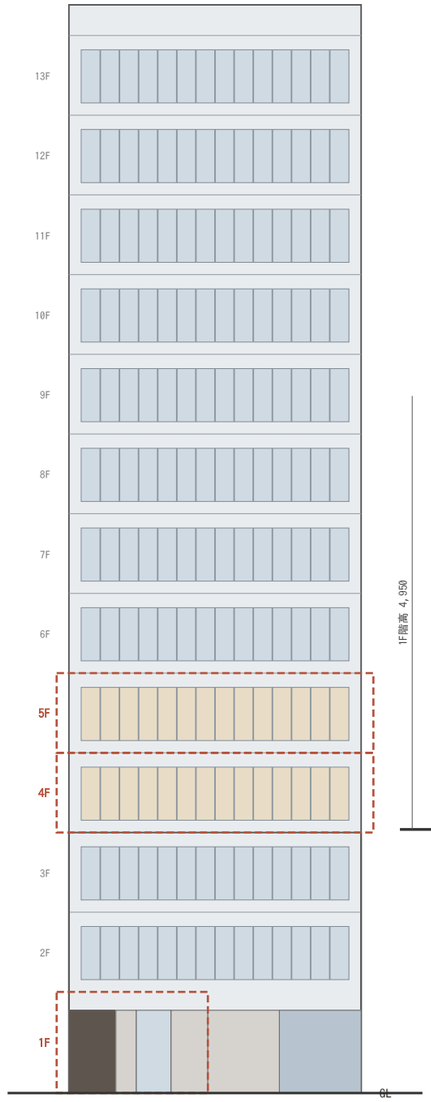

正面全体立面（Y1通り・模式）

S=1/300　赤破線＝当社区画

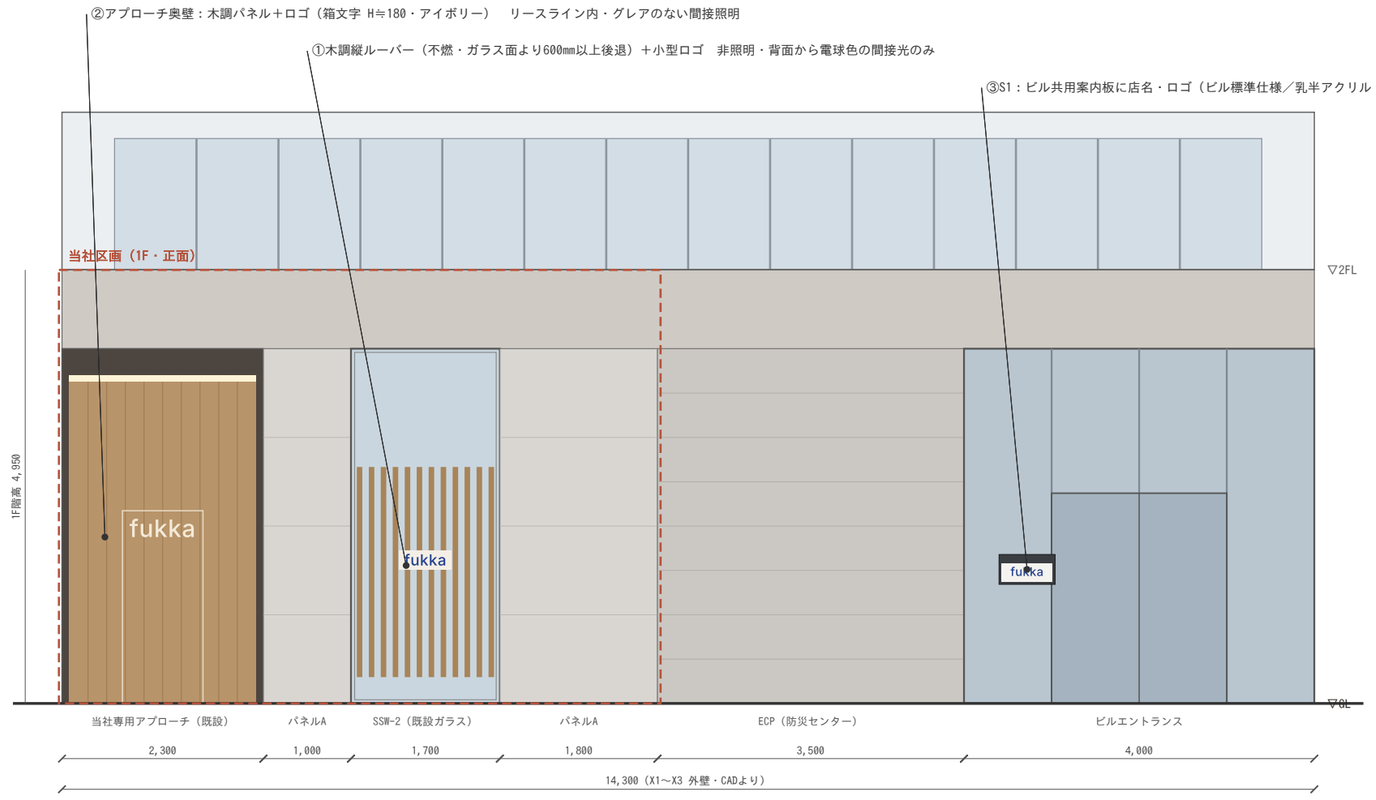

1階 正面部分立面図（サイン位置・使用素材）

S=1/70

サイン詳細（ビル指定仕様に準拠）



S1　W640×H340

ビル共用案内板（エントランス）
乳半アクリル＋ロゴ出力・LED内照
表示：ロゴのみ／約0.14㎡



S2　W300×H300

X1通り側・ビル指定位置
マットアクリル＋ダイノック
白切文字／約0.09㎡

外装サイン方針


（貸主ご意向：落ち着いた外観）

- 突出・袖看板、壁面大型看板は設けない
- ガラス面のフィルム・ポスター広告なし
- S1・S2以外の屋外サインなし
- 点滅・映像・赤色光・ネオン不使用
- 店名・ロゴのみ（価格・施術内容の広告なし）
- 電球色2700～3000Kの間接光、調光・タイマー
- ガラス面から600㎜以上離隔、既設サッシ無加工
- 表示面積 合計約0.35㎡（上限10㎡）
- 4・5F窓：防炎ロールスクリーンのみ

・1F階高4,950は貸主CAD（展開図 1FL→2FL）より。基準階階高3,900、2F以上の外装は完成予想CGからの模式表現。
・サイン位置・形状はビル側指定（内装マニュアル7-(6)）に準拠。最終仕様は運営管理者と協議のうえ承認を得る。
・正面の当社区画は既設アプローチ・SSW-2ガラス面を含む約6.8m（1階 98.36㎡区画）。ガラス面への熱割れ計算が必要なフィルム等は使用しない。

fukka 日本橋院（仮称） 出店計画 ／ 日本橋WASAMIビル	
外観立面図・サイン計画図 基本計画（出店企画書添付資料）　2026.10	S=1/300・1/70 No.A-04　A3

外装イメージ EXTERIOR IMAGE

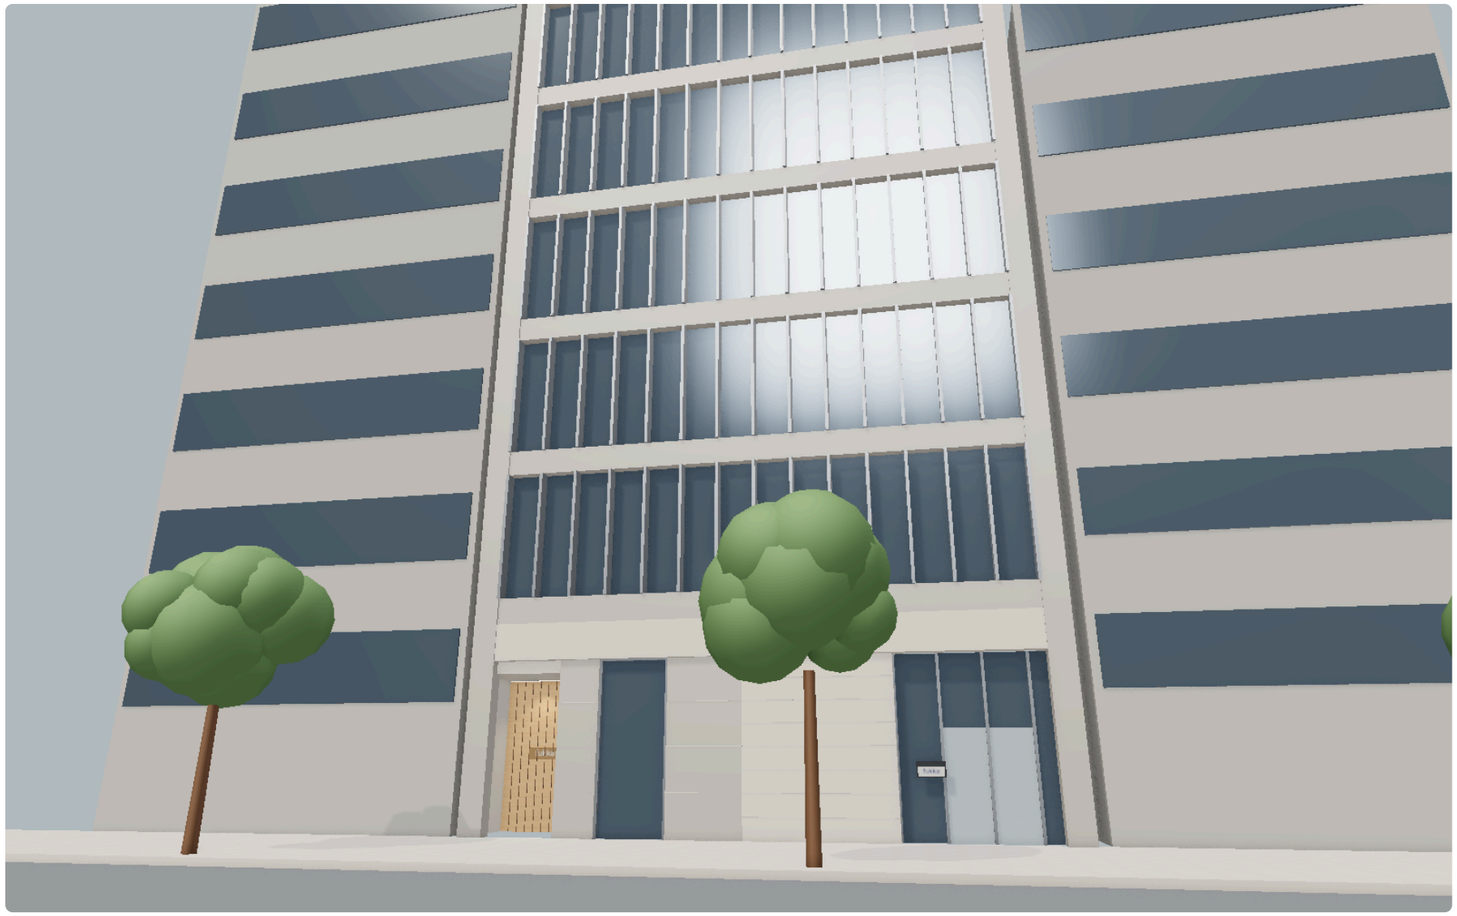

外装　正面（Y1通り）外観イメージ

既設の外装はそのまま、当社の表示は1F専用アプローチ奥の木調壁ロゴ、SSW-2ガラス奥の木調ルーバー、ビル共用案内板（S1）のみ。突出看板・ガラス面広告は設けません。



外装　1F 専用アプローチまわり

木調パネル＋アイボリーのロゴ（リースライン内）。照明は電球色の間接光のみで、夜間もまぶしさが出ない計画です。

サイン表示（合計 約0.35㎡）

S1 ビル案内板：ロゴのみ／S2 ビル指定位置：W300角プレート／1F窓：600mm後退ルーバー上の小型ロゴ（非照明）／4・5F窓：表示なし（ロールスクリーンのみ）


内装イメージ　1階（診察・処置・MRI・受付待合）

INTERIOR IMAGE 1F



1F **1F 受付・待合**

道路側アプローチから入ると正面に円形受付。銀座院と同じ木の天井リングと木目のロゴ壁。道路側ガラス面の内側は600mm後退した木調ルーバーで外からの視線をやわらげます。

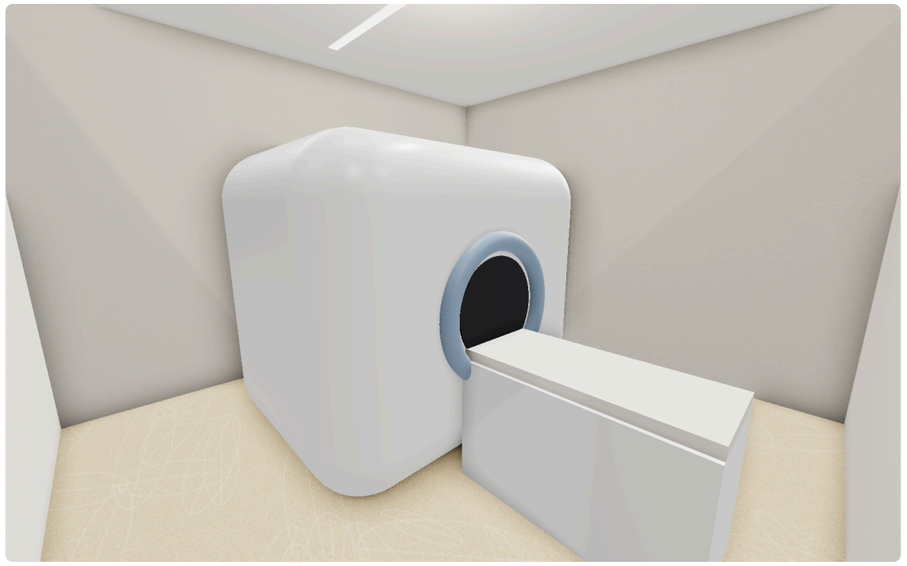

1F **MRI室**

磁気シールド工事を行う独立区画。操作室から観察窓で確認。



1F **1F 俯瞰**

受付待合／診察・処置／MRI（操作室・機械室）

内装イメージ　4階（受付・待合・更衣室・施術室）　INTERIOR IMAGE 4F



4F　4F 受付・待合（フロア中央の受付）
EVホールから自動ドアを入ると正面に受付。銀座院と同じ円形カウンター、木の天井リング、棚とロゴ壁の構成を拡大して再現しています。



4F　施術室前の通路
窓側に施術室を並べ、木目の引戸と白い壁で統一。



4F　施術室（約6.6㎡）
ベッド・スツール・荷物かご・棚。窓側で自然光を確保。

内装イメージ　5階（施術室・フリースペース・スタッフ休憩室）

INTERIOR IMAGE 5F



5F **5F フリースペース**

施術前後の待合、カウンセリング、小規模セミナーに使えるラウンジ。造作ベンチと丸テーブルで、銀座院と同じ素材・色を使います。



5F **5F 俯瞰**

施術室10室／フリースペース／スタッフ休憩室・更衣室・事務室



参考 **参考：銀座院（既存）**

トーン＆マナーはこの内装を基準にしています。

仕上表・ビル規定への対応　FINISH SCHEDULE / COMPLIANCE

仕上表（概略・基本計画段階）

部位	仕上	備考
床	タイルカーペット（防炎品・ベージュ系、銀座院同等柄）／MRI室・処置室：ビニル床シート	OAフロア（4・5F）上に施工
巾木	ソフト巾木 H60（ベージュ）	
壁	LGS＋PB12.5（不燃）下地　AEP塗装（白・塗り壁調）／受付背面：木目調不燃化粧板	施術室間仕切は上部開放の欄間式（欄間 h=500）
天井	既設天井（4・5F CH2,800）／1F：PB下地 AEP（CH約3,000）　受付上部：木目調リング（不燃）	既設防災設備（感知器・SP・非常照明）を活かす
建具	施術室：木目調不燃化粧板 引戸 W900×H2,100／エントランス：ガラス自動ドア	鍵1本をビル側へお預け
家具	受付カウンター（木目＋白天板）、待合チェア（ベージュ張地・木脚）、施術ベッド	家具は防炎・難燃材料を優先
照明	LEDライン照明・ダウンライト（電球色～温白色 3000～3500K、調光）	ビル電源容量内（1Φ約100VA/㎡、3Φ約200VA/㎡）
カーテン等	窓：防炎ロールスクリーン（アイボリー）	防炎ラベル縫付
MRI室	磁気シールド・RFシールド工事（専門業者）、専用電源・空調・チラー	床荷重・搬入経路・振動対策をビル側と協議

内装マニュアル（ビル規定）への対応

床荷重	1F 5,000N/㎡、4・5F 3,000N/㎡。重量物（MRI）は1Fに配置
間仕切	不燃材使用。欄間式とし、防災設備の追加が必要な場合はB工事で対応
避難経路	2～5F：EVホール～避難階段附室を廊下状に整備。防火扉の開閉を妨げる造作なし
ファサード	既設サッシ・ガラスは無加工、ガラス面から600mm以上離隔
サイン	ビル指定場所（S1・S2）のみ。点滅・映像・赤色光・ネオン不使用、店名ロゴのみ
設備	空調・電源は基準容量内。給排水（診察室・処置室の手洗い）は区画内の排水位置から計画、必要に応じ防水・漏水検知
用途	誘導用途区画のため診療所・施術所としての適合性を事前確認
提出図書	B工事指示書・基本設計図書：着工2.5か月前／実施設計図・工事申請書：着工1か月前

※本資料は出店審査用の基本計画です。面積は募集資料（1F 98.36㎡、4・5F 各G229.86㎡）による。図面寸法は募集図面・1F CADからの読取り値で、 実施設計時にビル側の白図・設備図に基づき確定します。パースはイメージで、実際の仕上・家具とは異なる場合があります。