

外観イメージ（正面・1F専用アプローチ）



4F 受付ロビー



1F 受付・待合

STORE OPENING PROPOSAL

出店企画書
添付資料

fukka

1F 整形外科ふっか 東京駅院

4・5F 整痛院ふっか 東京駅院

物件：日本橋WASAMIビル

東京都中央区日本橋三丁目（JR東京駅 徒歩1分）

1階：店舗区画 98.36㎡（約29.75坪）

4階・5階：各 G229.86㎡（約69.53坪）

合計：約168.8坪／施術室 20室・MRI室



5F フリースペース

2026年10月　基本計画

計画概要 PLAN OVERVIEW

168.8坪
1F 29.75坪＋4F・5F 各69.53坪

20
施術室（各 約4畳）

1.5T
MRI（富士フイルム）1F

1分
JR東京駅（22番出口）徒歩

コンセプト

銀座院の空間（白い塗り壁、木目、ベージュのカーペット、中央の円形受付と木の天井リング）をそのまま拡大し、施術室を増やした「銀座院の大型版」。外観はビルの意匠を活かし、看板を目立たせない落ち着いた表現とします。

フロア構成

1F 98.36㎡ 約29.75坪	待合、診察室、MRI機械室、処置室、MRI更衣（1名）、MRI操作室、MRI検査室（電磁シールド）
4F 229.86㎡ 約69.53坪	施術室 10室（各約4畳）、更衣室（男性）、更衣室（女性）パウダー付、受付・待合ロビー、ドリンクコーナー、相談室
5F 229.86㎡ 約69.53坪	施術室 10室（各約4畳）、スタッフ休憩室、スタッフ更衣（男）、スタッフ更衣（女）、フリースペース、物品・リネン庫（既設キッチン含む）

動線

検査・診察：道路 → 1F専用アプローチ → 受付 → 診察・MRI
施術：ビルEV → 4F受付 → 更衣室 → 4F／5F施術室
スタッフ：5F休憩室・更衣室・物品庫を拠点に各階へ














1階 平面計画図（受付待合・診察室・処置室・MRI室）

貸室面積 98.36㎡（約29.75坪）

← 正面道路（Y1通り・歩道）

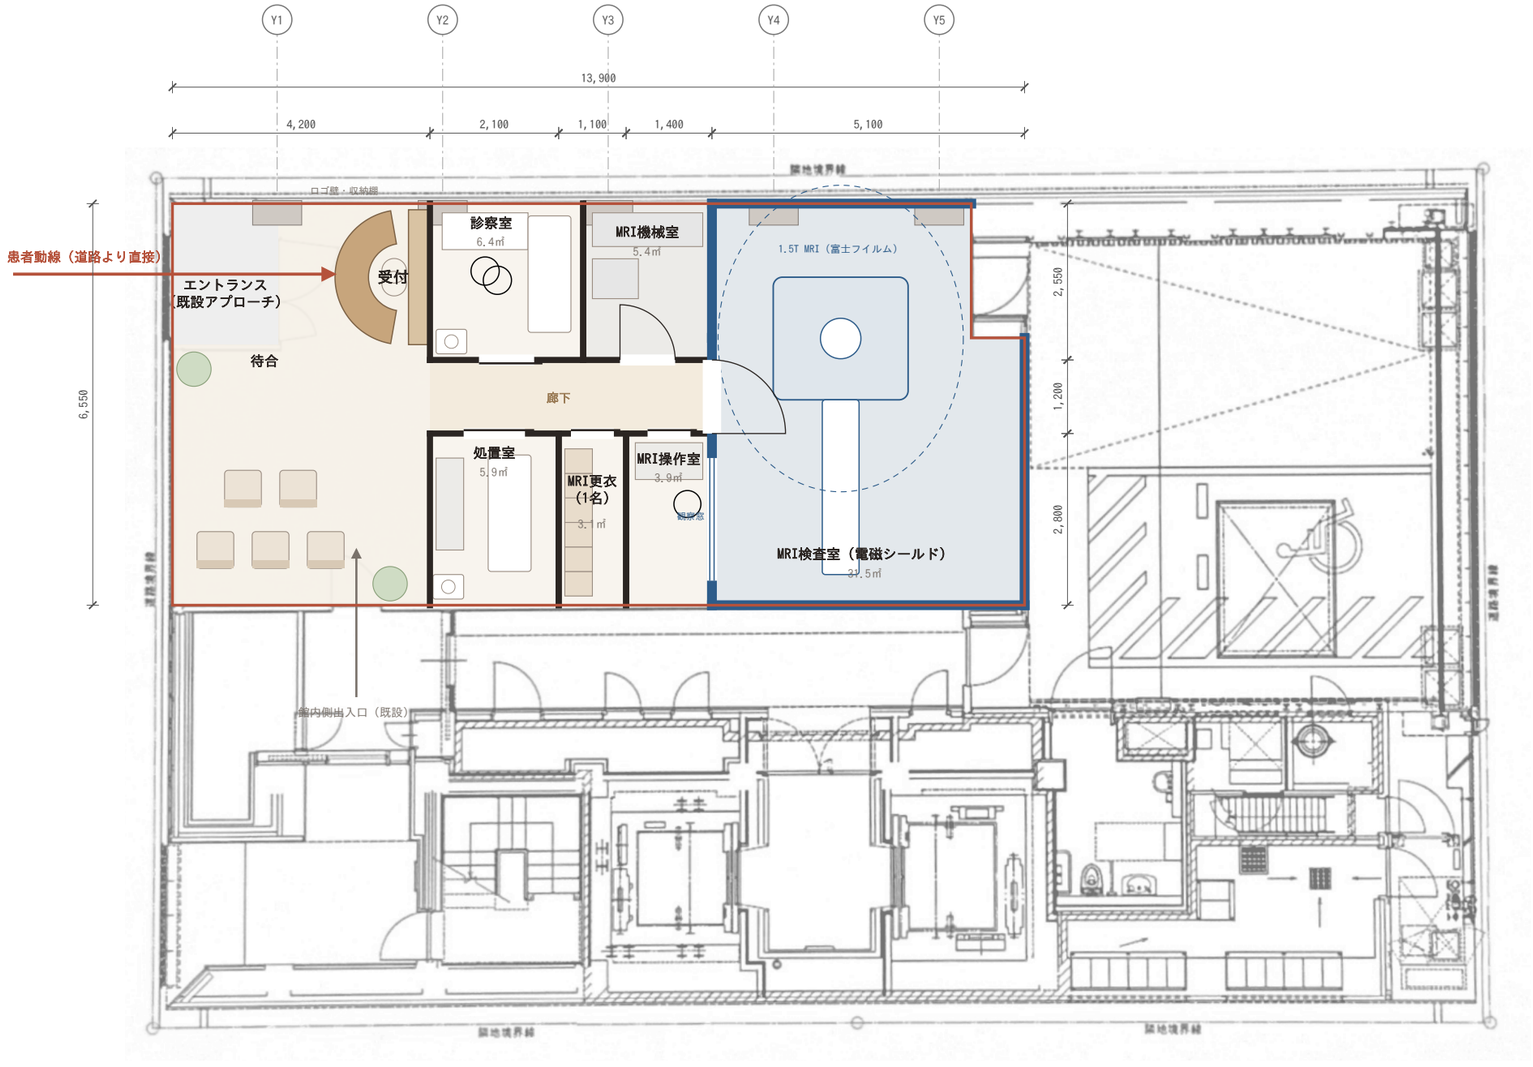

図の向き

左：正面道路（Y1側）

上：X1通り側　※真北は要確認

- 貸室 98.36㎡（約29.75坪）
- 診察・処置・操作・更衣
- MRI室（シールド工事）
- 機械室
- 既設アプローチ（区画内）

諸室面積表（内法・概算）

診察室	6.4㎡
MRI機械室	5.4㎡
処置室	5.9㎡
MRI更衣（1名）	3.1㎡
MRI操作室	3.9㎡
MRI検査室（電磁シールド）	31.5㎡

・下図（グレー）は貸主提供の募集図面（1階 店舗区画）。赤線＝貸室区画（98.36㎡）、着色部・室配置が当社計画（C工事）。
・MRI：富士フイルム製1.5T（ゼロヘリウム型想定・クエンチ配管不要）。検査室約31.5㎡・機械室約5.4㎡・操作室約3.9㎡。破線は5ガウスライン目安。機種仕様書で要確認。
・床荷重5,000N/㎡の1Fに配置。荷重分散架台・搬入経路（マシンハッチ1,830×2,500）・振動・騒音・電源容量をビル側と協議。
・道路側ガラス面から600mm以内には造作・サインを設けない（内装マニュアル7-(7)）。
・トイレは館内共用トイレを利用。間仕切・内装材は全て不燃材、カーペットは防炎品。

整形外科ふっか／整痛院ふっか 東京駅院 出店計画 ／ 日本橋WASAMIビル	
1階 平面計画図（受付待合・診察室・処置室・MRI室） 基本計画（出店企画書添付資料）　2026.10	S=1/100 No.A-01　A3

4階 平面計画図（受付ロビー・更衣室・施術室10室）

貸室面積 G229.86㎡（約69.53坪）

← 正面道路（Y1通り）



※コアは募集図面（4・5階）をもとに作図。実寸はビル側図面にて要確認

図の向き

左：正面道路（Y1側）
上：X1通り側　※真北は要確認

- 貸室 G229.86㎡（約69.53坪）
- 施術室（銀座院仕様）
- 個室（更衣・カウンセリング等）
- バックヤード
- 廊下・通路（階段・トイレへ）
- 共用部（コア）

諸室面積表（内法・概算）

施術室 × 10室	各6.0〜6.6㎡
更衣室（男性）	6.6㎡
更衣室（女性）パウダー付	11.4㎡
相談室	4.0㎡

・施術室 4F 10室 ＋ 5F 10室 ＝ 計20室（要件15〜20室）。各室 約6.5㎡（約4畳）。間仕切は上部開放の欄間式（欄間h=500）。
・受付はEVホール正面・フロア中央に大きく配置（銀座院と同じ円形カウンター＋木の天井リング）。ロビーは柱・壁のない開放的な空間。
・特別避難階段・共用トイレへは廊下・通路で直接つながる計画（EVホール〜階段附室を廊下状に確保：内装マニュアル6-(7)）。
・X1側（施術室側）は窓なし。通路は両側居室部分を有効1,600mm（令119条）。平面は募集図面をもとに作図、実施設計時に白図で確定。

整形外科ふっか／整痛院ふっか 東京駅院 出店計画 ／ 日本橋WASAMIビル	
4階 平面計画図（受付ロビー・更衣室・施術室10室） 基本計画（出店企画書添付資料）　2026.10	S=1/100 No.A-02　A3

5階 平面計画図（施術室10室・フリースペース・スタッフ休憩室）

貸室面積 G229.86㎡（約69.53坪）

← 正面道路（Y1通り）



※コアは募集図面（4・5階）をもとに作図。実寸はビル側図面にて要確認

図の向き

左：正面道路（Y1側）
上：X1通り側　※真北は要確認

- 貸室 G229.86㎡（約69.53坪）
- 施術室（銀座院仕様）
- 個室（更衣・カウンセリング等）
- バックヤード
- 廊下・通路（階段・トイレへ）
- 共用部（コア）

諸室面積表（内法・概算）

施術室 × 10室	各6.0〜6.6㎡
スタッフ休憩室	16.0㎡
スタッフ更衣（男）	4.2㎡
スタッフ更衣（女）	4.2㎡
物品・リネン庫（既設キッチン含む）	8.7㎡

・施術室 10室（各 約6.5㎡・約4畳）、フリースペース、スタッフ休憩室・スタッフ更衣室（男女）・物品庫を5階に集約。
・フリースペースは施術前後の待合・カウンセリング・セミナー兼用のラウンジ。
・特別避難階段・共用トイレへは廊下・通路で直接つながる計画（4Fと同一）。
・X1側（施術室側）は窓なし。平面形状は募集図面（4・5階 G229.86㎡）をもとに作図、実施設計時にビル側白図で寸法を確定。


整形外科ふっか／整痛院ふっか 東京駅院 出店計画 ／ 日本橋WASAMIビル

5階 平面計画図（施術室10室・フリースペース・スタッフ休憩室） S=1/100

基本計画（出店企画書添付資料） 2026.10


No.A-03 A3

外観立面図・サイン計画図（正面 Y1通り）

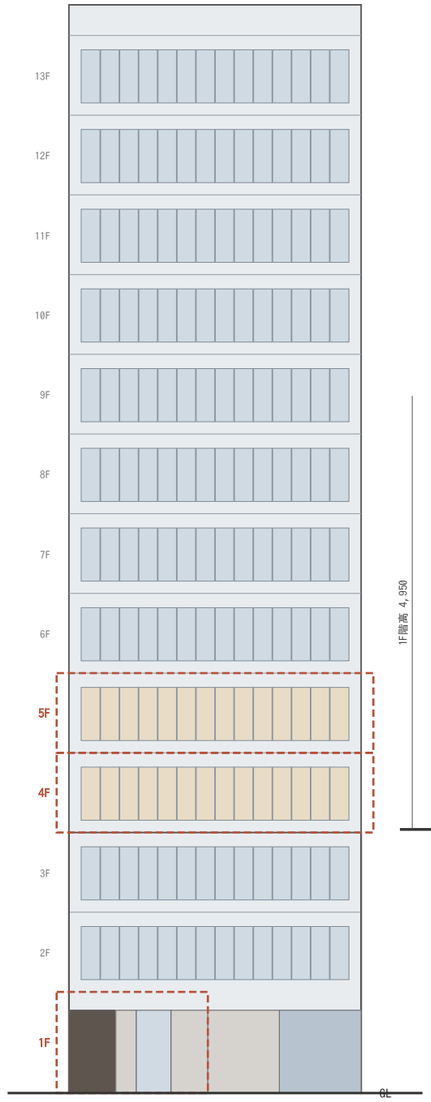

正面全体立面（Y1通り・模式）

S=1/300　赤破線＝当社区画

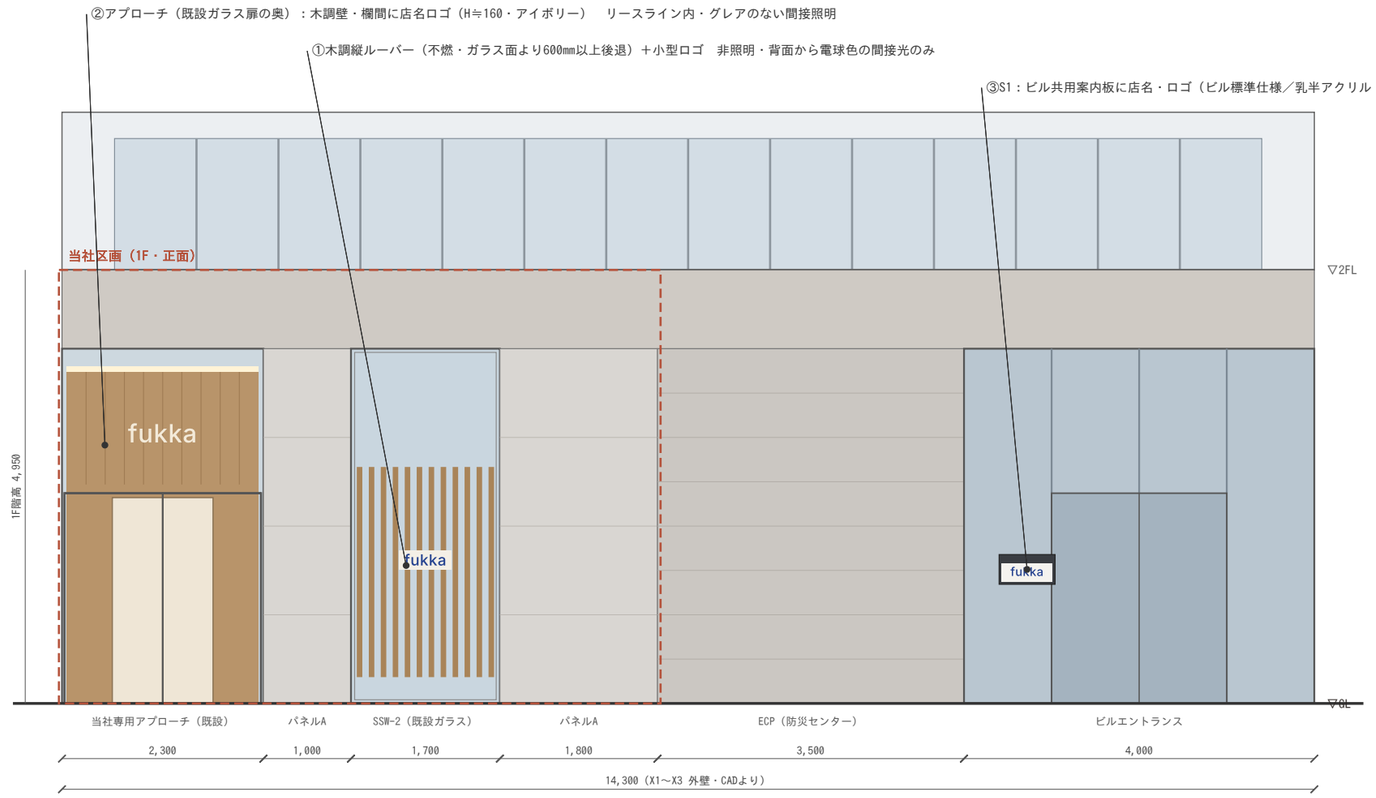

1階 正面部分立面図（サイン位置・使用素材）

S=1/70

サイン詳細（ビル指定仕様に準拠）



S1　W640×H340

ビル共用案内板（エントランス）
乳半アクリル＋ロゴ出力・LED内照
表示：ロゴのみ／約0.14㎡



S2　W300×H300

X1通り側・ビル指定位置
マットアクリル＋ダイノック
白切文字／約0.09㎡

外装サイン方針

（貸主ご意向：落ち着いた外観）


- 突出・袖看板、壁面大型看板は設けない
- ガラス面のフィルム・ポスター広告なし
- S1・S2以外の屋外サインなし
- 点滅・映像・赤色光・ネオン不使用
- 店名・ロゴのみ（価格・施術内容の広告なし）
- 電球色2700～3000Kの間接光、調光・タイマー
- ガラス面から600㎜以上離隔、既設サッシ無加工
- 表示面積 合計約0.35㎡（上限10㎡）
- 4・5F窓：防炎ロールスクリーンのみ

・1F階高4,950は貸主CAD（展開図 1FL→2FL）より。基準階階高3,900、2F以上の外装は完成予想CGからの模式表現。
・サイン位置・形状はビル側指定（内装マニュアル7-(6)）に準拠。最終仕様は運営管理者と協議のうえ承認を得る。
・正面の当社区画は既設アプローチ・SSW-2ガラス面を含む約6.8m（1階 98.36㎡区画）。ガラス面への熱割れ計算が必要なフィルム等は使用しない。


整形外科ふっか／整痛院ふっか 東京駅院 出店計画 ／ 日本橋WASAMIビル	
外観立面図・サイン計画図 基本計画（出店企画書添付資料）　2026.10	S=1/300・1/70 No.A-04　A3

1F 専用アプローチ（風除室）詳細図

平面詳細　S=1/30

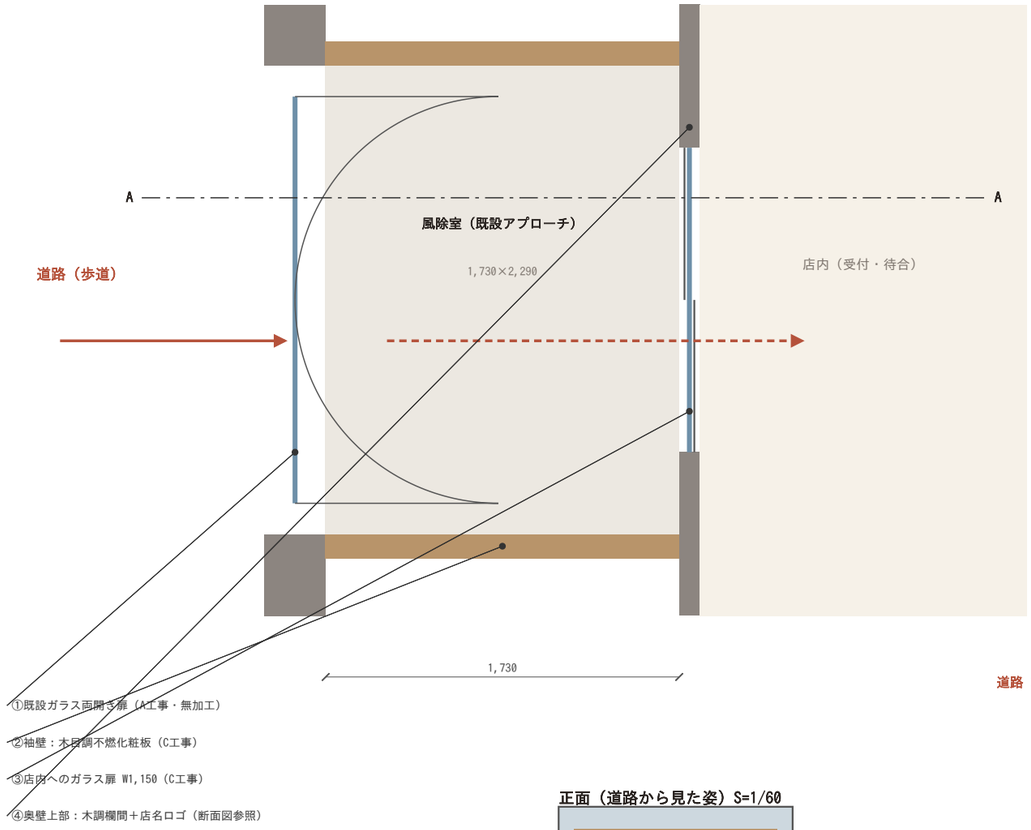


断面詳細 A-A　S=1/30

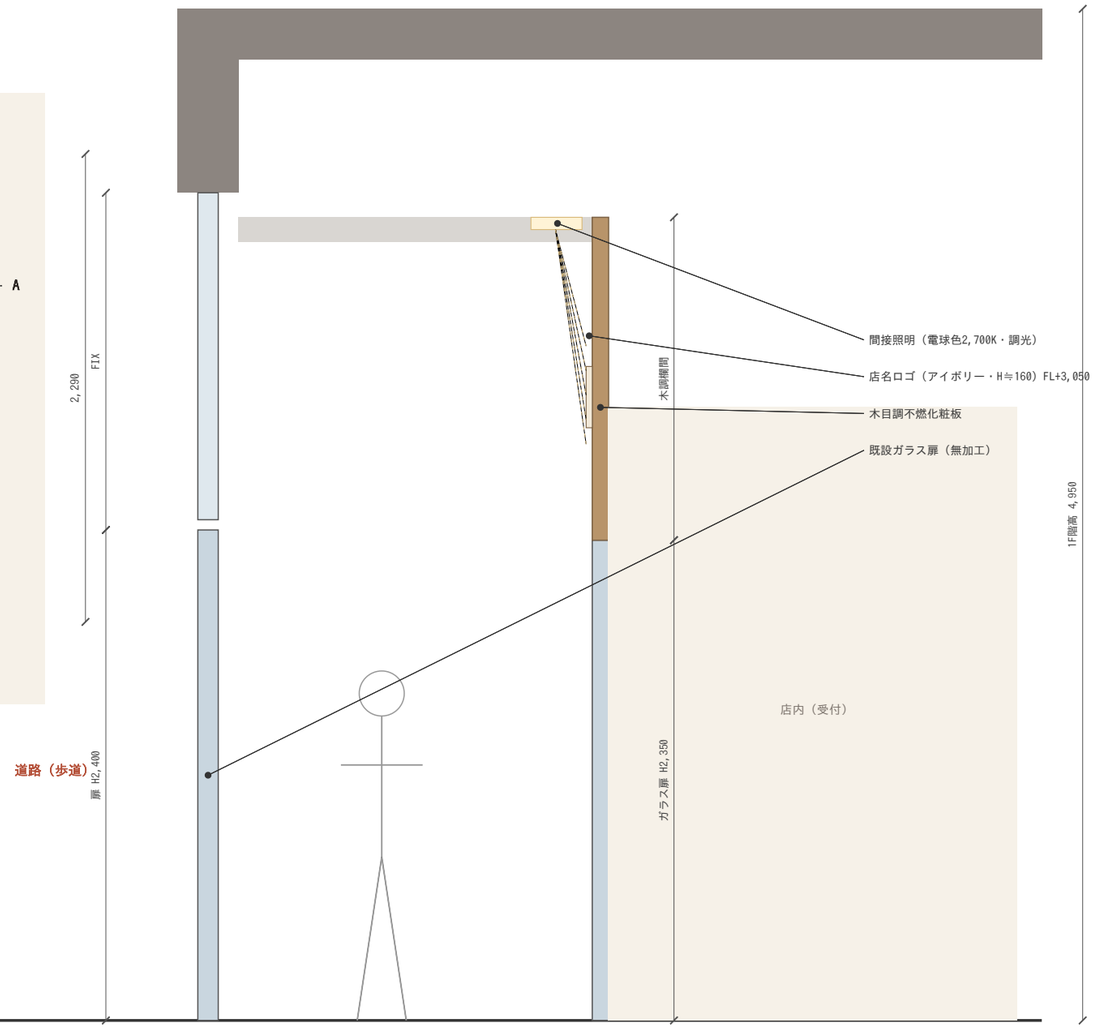

→ 外装イメージ（P.8）と同一


正面（道路から見た姿）S=1/60

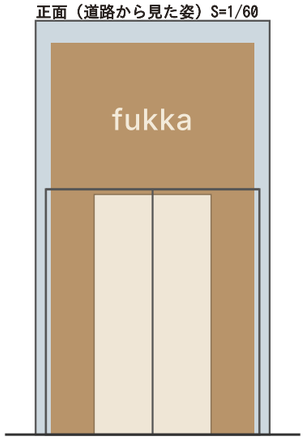

・既設アプローチ（風除室）は区画内。道路側のガラス両開き扉・上部FIXガラスは既設（A工事）のまま使用し、加工しない。
・当社工事（C工事）は、奥の店内へのガラス扉（自動または手動）、木調の袖壁・欄間仕上、店名ロゴ、間接照明。
・ロゴは道路側ガラス面から1,700mm以上奥に位置し、ガラス面から600mm以上の離隔を確保。グレアのない電球色の間接光のみ。
・床は既設の仕上・スロープ（バリアフリー）をそのまま使用。寸法は1F CAD・募集図面からの読取り値（実施設計時に確定）。

整形外科ふっか／整痛院ふっか 東京駅院 出店計画 ／ 日本橋WASAMIビル	
1F専用アプローチ 詳細図（平面・断面・正面） 基本計画（出店企画書添付資料）　2026.10	S=1/30 No.A-05　A3

外装イメージ EXTERIOR IMAGE

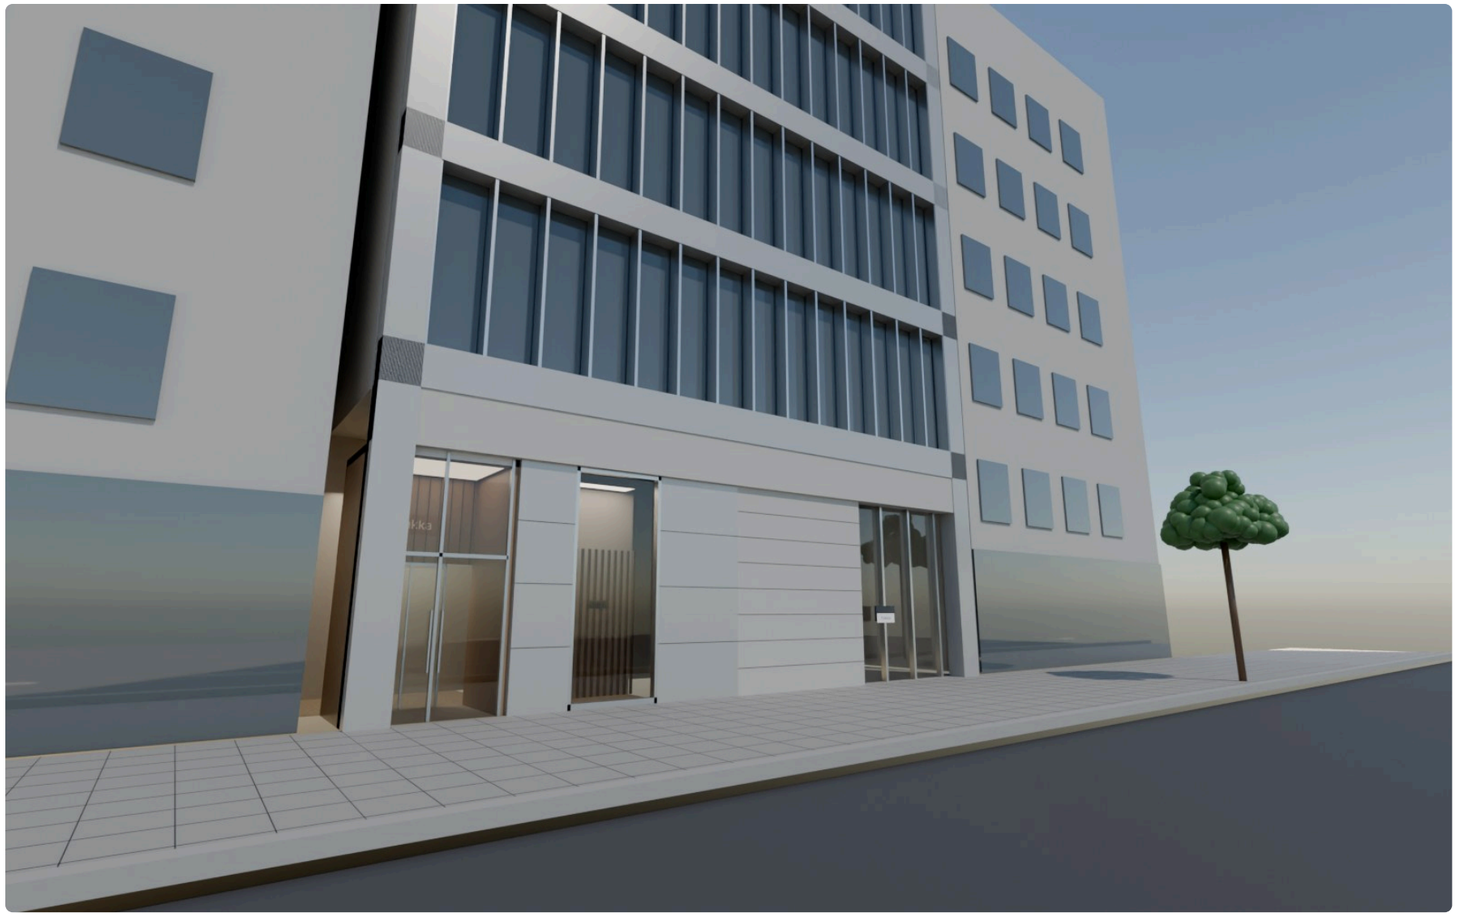

外装　正面（Y1通り）外観イメージ

ビル既設の外装はそのまま。当社の表示は、1F専用アプローチ奥の木調欄間のロゴ、SSW-2ガラス奥（600mm後退）の木調ルーバー上の小型ロゴ、ビル共用案内板（S1）のみ。突出看板・ガラス面広告はありません（立面図 A-04 と同一仕様）。



外装　1F 専用アプローチまわり

既設ガラス扉の奥に木調の袖壁・欄間と店名ロゴ。電球色の間接光のみで、夜もまぶしさのない落ち着いた表情です。



正面全景

4・5F窓面は内側の防炎ロールスクリーンのみで、サイン表示はありません。

内装イメージ　1階（受付待合・診察・処置・MRI）

INTERIOR IMAGE 1F




1F　1F 受付・待合

専用アプローチから入ると正面に円形受付。銀座院と同じ木の天井リングとロゴ壁。待合は少人数でゆったりと。道路側ガラスの内側は600㎜後退した木調ルーバーで外からの視線をやわらげます。





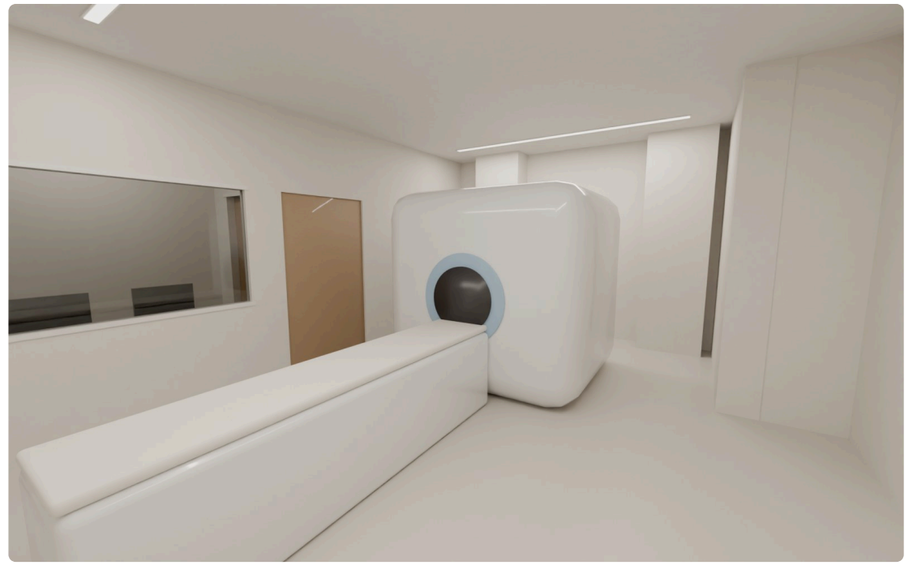

1F　MRI検査室（平面図A-01と同形状・約31.5㎡）

富士フイルム製1.5T MRIを想定。電磁シールド工事を行う独立区画。操作室から観察窓で確認。



1F　診察室（約6.4㎡）

医師の診察デスクとモニター、診察ベッド、手洗い。検査画像をその場で説明できます。

内装イメージ　4階（受付ロビー・更衣室・施術室）　INTERIOR IMAGE 4F



4F　4F 受付ロビー

EVホールから続く柱・壁のない開放的なロビー。中央に大きな円形受付、木の天井リング、棚とロゴ壁で銀座院の雰囲気を再現。待合いすはゆとりをもって配置。




4F　EVホール側から見た受付

エレベーターを降りて正面に受付が見える配置です。





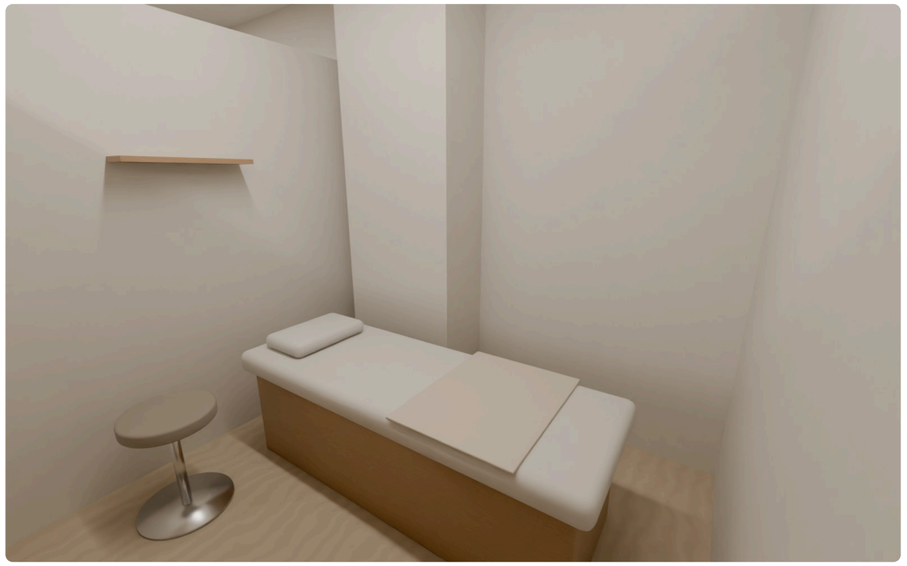

4F　施術室（約6.6㎡・約4畳）

ベッド・スツール・荷物かご・フック。木目の引戸で統一（窓なし）。

内装イメージ　5階（施術室・フリースペース・スタッフエリア）

INTERIOR IMAGE 5F



5F **5F フリースペース**

施術前後の待合・カウンセリング・セミナーに使えるラウンジ。造作ベンチと丸テーブル、銀座院と同じ素材と色。



5F **スタッフ休憩室（約18㎡）**

道路側の窓に面した明るい休憩室。ミニキッチン・冷蔵庫付き。スタッフ更衣室（男女）・物品庫も5階に集約。



5F **5F 俯瞰**

施術室10室／フリースペース／スタッフ休憩室・更衣室／物品・リネン庫

銀座院のご紹介（整痛院ふっか）　GINZA CLINIC


銀座院 待合・受付（実写）


受付カウンター


個室（施術・カウンセリング）


カウンセリング


施術・説明


講演・セミナー活動

3万件超
グループ累計施術件数

9院
全国展開（福岡・東京ほか）

2016年
開業（2023年 法人化）

2025年
銀座 新モデル大型院を開院

腰痛・坐骨神経痛など慢性的な痛み・しびれに特化した「整痛院」。2025年には大阪・関西万博のステージで「整痛」の取り組みを講演。 東京駅院では、銀座院の施術モデルに**1.5T MRIを備えた医療フロア**を加え、検査から施術まで一貫して提供します。 東京駅院の内装は、写真の銀座院（白い塗り壁・木目・ベージュのカーペット・円形受付）をそのまま踏襲します。

会社・銀座院の概要（公開情報）

ブランド	整痛院ふっか（痛み・しびれ専門）
運営	株式会社ふっか（代表取締役 松田 圭太・理学療法士）
沿革	2016年8月 開業（福岡）／2023年6月 法人化
店舗	全国9院（2025年5月時点）
銀座院	2025年6月6日開院　東京都中央区銀座3-13-19 3F（東銀座駅 徒歩約2分）
営業	9:00〜21:00（不定休）・完全予約制
施術	独自のMSMメソッド（手技・運動療法・認知行動療法の考え方）
料金	初回 12,000円（税込）／初回約120分・2回目以降約30分

東京駅院のイメージ（参考）



銀座院の内装パース。東京駅院も同じトーン＆マナーで計画。

写真・情報出典：整痛院ふっか公式サイト（fukka.jp）、整痛院ふっか銀座院ページ、PR TIMES（株式会社ふっか プレスリリース）。数値は公表時点のもの。

仕上表・ビル規定への対応 FINISH SCHEDULE / COMPLIANCE

仕上表（概略・基本計画段階）

部位	仕上	備考
床	タイルカーペット（防炎品・防炎表示付、ベージュ系・銀座院同等柄）／MRI室・処置室：ビニル床シート	4・5F：既設OAフロア（h=100）上に施工
巾木	ソフト巾木 H60（ベージュ）	
壁	軽量鉄骨下地＋石膏ボード（不燃）AEP塗装（白・塗り壁調）／受付背面：木目調不燃化粧板	施術室間仕切は上部開放の欄間式（欄間 h=500）
天井	4・5F：既設天井（CH2,800）／1F：直天（想定FL+3,700）のため石膏ボード天井を新設（CH約3,000）　受付上部：木目調リング（不燃）	既設の感知器・スプリンクラー・非常照明の機能を妨げない
建具	施術室：木目調不燃化粧板 引戸 W900×H2,100／MRI室：シールド扉（専門業者）	鍵1本をビル側へお預け
家具	受付カウンター（木目＋白天板）、待合いす（ベージュ張地・木脚）、施術ベッド	防災設備の機能を妨げない配置
照明	LEDライン照明・ダウンライト（電球色〜温白色 3,000〜3,500K、調光）	4・5F電気容量：1Φ約100VA/㎡、3Φ約200VA/㎡（募集資料）
カーテン等	4・5F道路側窓：防炎ロールスクリーン（アイボリー）	防炎物品（防炎ラベル縫付）
MRI室	1.5T MRI（富士フイルム）：電磁（RF）シールド工事・必要に応じ磁気シールド（専門業者）、専用空調・チラー、荷重分散架台	ゼロヘリウム型はクエンチ配管不要。重量・振動・騒音・電源容量はビル側と事前協議

内装マニュアル（ビル規定）への対応

床荷重	1〜3F 5,000N/㎡、4・5F 3,000N/㎡（室内全体の荷重制限は別途）。重量物のMRIは1Fに配置し、重量・脚部・配置を事前相談
間仕切	不燃材を使用。上部開放の欄間式（欄間 h≥500）とし、防災設備の追加が必要な場合はB工事で対応
廊下幅	両側に居室が面する通路は有効1,600mm、その他の廊下は1,200mm以上を確保（建築基準法施行令119条）
避難経路	2〜5F：EVホールから避難階段附室まで廊下状に整備。当計画は廊下・通路で特別避難階段・共用トイレに直結。EVホール入口の防火扉の開閉を妨げる造作・什器なし
ファサード・サイン	既設サッシ・ガラスは無加工、ガラス面から600mm程度離隔。サインはビル指定位置（S1・S2）のみ、店名・ロゴに限定。点滅・映像・赤色光・露出ネオン不使用、表示面積10㎡以下
電気・空調	設定容量内で計画（設定容量を超える電源増設・保安電源の増設は不可）。空調吹出口・吸込口の機能を妨げない
特殊設備	騒音・振動・熱を発生する機器（MRI装置・チラー等）はビル側の承認を得て設置。躯体のはつり・ホールインアンカーは原則不可
給排水	4・5F：給水 PS内バルブ止め（40A）、排水 区画内スラブ上ころがしキャップ止め（100A）。漏水対策（防水・漏水検知）を指示に従い実施
点検口・収納	共用配管・配線部に点検口を設置。共用倉庫・従業員ロッカーはないため、店舗内（5F）に確保
用途	誘導用途区画（日本橋・東京駅前地区）のため、診療所・施術所としての用途適合性を事前に確認
提出図書	B工事指示書・基本設計図書：着工2.5か月前（B工事見積は1か月）／工事申請書・実施設計図：着工1か月前／竣工図：竣工後1か月以内

※出典：内装マニュアル（2026年8月7日発行）、募集資料。本資料は出店審査用の基本計画です。図面寸法は募集図面・1F CADからの読取り値で、実施設計時にビル側の白図・設備図に基づき確定します。パースはイメージで、実際の仕上・家具とは異なる場合があります。