
外観イメージ（正面・1F玄関ポーチ）



4F 受付ロビー


1F 受付・待合

STORE OPENING PROPOSAL

出店企画書
添付資料

fukka

1F 整形外科ふっか 東京駅院

4・5F 整痛院ふっか 東京駅院

物件：日本橋WASAMIビル

東京都中央区日本橋三丁目（JR東京駅 徒歩1分）

1階：店舗区画 98.36㎡（約29.75坪）

4階・5階：各 G229.86㎡（約69.53坪）

合計：約168.8坪／施術室 20室・診察室4室・処置室3室


5F フリースペース

2026年10月　基本計画

計画概要 PLAN OVERVIEW

168.8坪
1F 29.75坪＋4F・5F 各69.53坪

20
施術室（各 約4畳）

4＋3
1F 診察室4室・処置室3室

1分
JR東京駅（22番出口）徒歩

コンセプト

銀座院の空間（白い塗り壁、木目、ベージュのカーペット、中央の円形受付と木の天井リング）をそのまま拡大し、施術室を増やした「銀座院の大型版」。外観はビルの意匠を活かし、看板を目立たせない落ち着いた表現とします。

フロア構成

1F 98.36㎡ 約29.75坪	待合（15席）、診察室1、診察室2、診察室3、診察室4、処置室1、処置室2、処置室3、スタッフ室、倉庫
4F 229.86㎡ 約69.53坪	施術室 10室（各約4畳）、更衣室（男性）、更衣室（女性）パウダー付、受付・待合ロビー、ドリンクコーナー、相談室
5F 229.86㎡ 約69.53坪	施術室 10室（各約4畳）、スタッフ休憩室、スタッフ更衣（男）、スタッフ更衣（女）、フリースペース、物品・リネン庫（既設キッチン含む）

動線

診察：道路 → 1F玄関ポーチ（既設扉）→ 受付・待合 → 診察室・処置室
施術：ビルEV → 4F受付 → 更衣室 → 4F／5F施術室
スタッフ：5F休憩室・更衣室・物品庫を拠点に各階へ



道路から玄関ポーチ（既設扉）で直接入れる医療フロア。受付・待合15席（道路側ガラス面に木調ルーバー）・診察室4室・処置室3室





EVを降りると正面に円形受付の開放的なロビー。男女更衣室・施術室10室






施術室10室・フリースペース。スタッフ休憩室・更衣室・物品庫を集約



1階 平面計画図（受付・待合・診察室・処置室）

貸室面積 98.36㎡（約29.75坪）

← 正面道路（Y1通り・歩道）

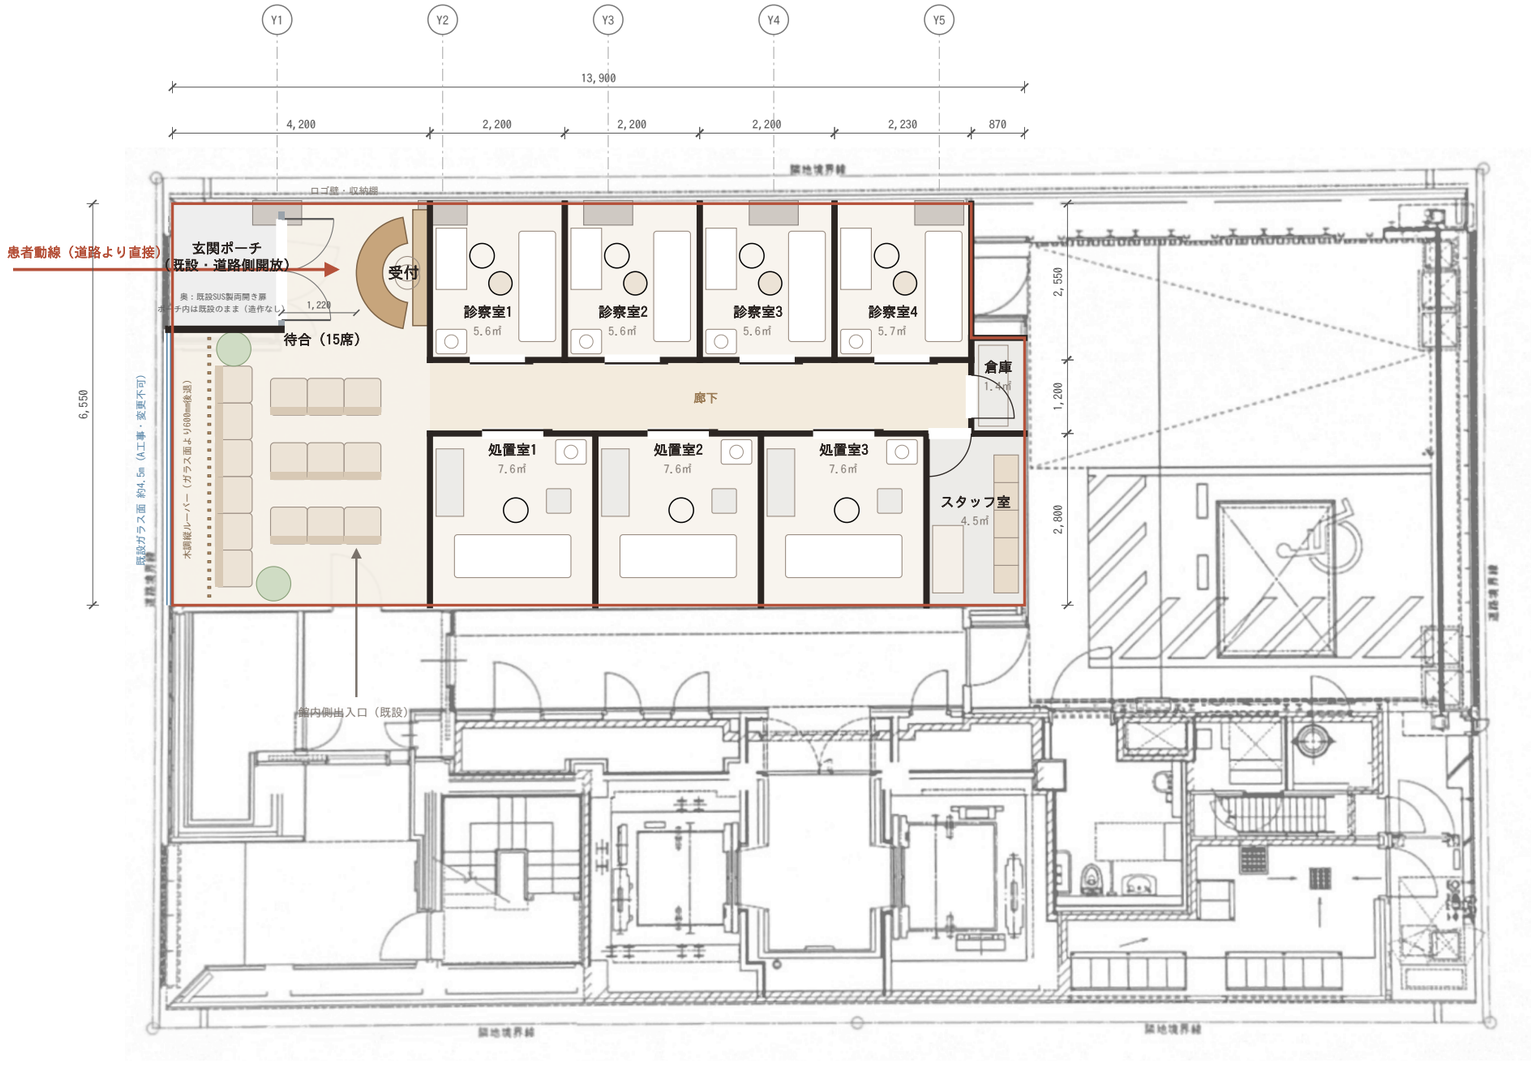

図の向き

左：正面道路（Y1側）
上：X1通り側　※真北は要確認

- 貸室 98.36㎡（約29.75坪）
- 診察室・処置室
- 廊下
- スタッフ室・倉庫
- 玄関ポーチ（既設・区画内）

諸室面積表（内法・概算）

診察室1	5.6㎡
診察室2	5.6㎡
診察室3	5.6㎡
診察室4	5.7㎡
処置室1	7.6㎡
処置室2	7.6㎡
処置室3	7.6㎡
スタッフ室	4.5㎡
倉庫	1.4㎡

・下図（グレー）は貸主提供の募集図面（1階 店舗区画）。赤線＝貸室区画（98.36㎡）、着色部・室配置が当社計画（C工事）。
・部屋構成：受付、待合（最大15名・15席）、診察室4室（各約5.6㎡）、処置室3室（各約7.6㎡）、スタッフ室・倉庫。診察室・処置室は全室に手洗い器。
・受付は玄関の既設扉の正面（扉から1,220mm）。待合は道路側ガラス面に面し、廊下（幅1,200）から診察室・処置室へ。館内側出入口からも廊下へ直接つながる。
・玄関ポーチ（道路側開放）・奥の既設SUS両開き扉・道路側ガラス面（約4.5m）は既設（A工事）のまま。ガラス面から600mm内側に木調縦ルーバー、600mm以内に造作・サインなし（内装マニュアル7-(7)）。
・トイレは館内共用トイレを利用。間仕切・内装材は全て不燃材、カーペットは防炎品。

整形外科ふっか／整痛院ふっか 東京駅院 出店計画 ／ 日本橋WASAMIビル	
1階 平面計画図（受付・待合・診察室・処置室） 基本計画（出店企画書添付資料）　2026.10	S=1/100 No.A-01　A3

4階 平面計画図（受付ロビー・更衣室・施術室10室）

貸室面積 G229.86㎡（約69.53坪）

← 正面道路（Y1通り）



※コアは募集図面（4・5階）をもとに作図。実寸はビル側図面にて要確認

図の向き

左：正面道路（Y1側）
上：X1通り側　※真北は要確認

- 貸室 G229.86㎡（約69.53坪）
- 施術室（銀座院仕様）
- 個室（更衣・カウンセリング等）
- バックヤード
- 廊下・通路（階段・トイレへ）
- 共用部（コア）

諸室面積表（内法・概算）

施術室 × 10室	各6.0〜6.6㎡
更衣室（男性）	6.6㎡
更衣室（女性）パウダー付	11.4㎡
相談室	4.0㎡

・施術室 4F 10室 ＋ 5F 10室 ＝ 計20室（要件15〜20室）。各室 約6.5㎡（約4畳）。間仕切は上部開放の欄間式（欄間h=500）。
・受付はEVホール正面・フロア中央に大きく配置（銀座院と同じ円形カウンター＋木の天井リング）。ロビーは柱・壁のない開放的な空間。
・特別避難階段・共用トイレへは廊下・通路で直接つながる計画（EVホール〜階段附室を廊下状に確保：内装マニュアル6-(7)）。
・X1側（施術室側）は窓なし。通路は両側居室部分を有効1,600mm（令119条）。平面は募集図面をもとに作図、実施設計時に白図で確定。

整形外科ふっか／整痛院ふっか 東京駅院 出店計画 ／ 日本橋WASAMIビル	
4階 平面計画図（受付ロビー・更衣室・施術室10室） 基本計画（出店企画書添付資料）　2026.10	S=1/100 No.A-02　A3

5階 平面計画図（施術室10室・フリースペース・スタッフ休憩室）

貸室面積 G229.86㎡（約69.53坪）

← 正面道路（Y1通り）



※コアは募集図面（4・5階）をもとに作図。実寸はビル側図面にて要確認

図の向き

左：正面道路（Y1側）
上：X1通り側　※真北は要確認

- 貸室 G229.86㎡（約69.53坪）
- 施術室（銀座院仕様）
- 個室（更衣・カウンセリング等）
- バックヤード
- 廊下・通路（階段・トイレへ）
- 共用部（コア）

諸室面積表（内法・概算）

施術室 × 10室	各6.0〜6.6㎡
スタッフ休憩室	16.0㎡
スタッフ更衣（男）	4.2㎡
スタッフ更衣（女）	4.2㎡
物品・リネン庫（既設キッチン含む）	8.7㎡

・施術室 10室（各 約6.5㎡・約4畳）、フリースペース、スタッフ休憩室・スタッフ更衣室（男女）・物品庫を5階に集約。
・フリースペースは施術前後の待合・カウンセリング・セミナー兼用のラウンジ。
・特別避難階段・共用トイレへは廊下・通路で直接つながる計画（4Fと同一）。
・X1側（施術室側）は窓なし。平面形状は募集図面（4・5階 G229.86㎡）をもとに作図、実施設計時にビル側白図で寸法を確定。


整形外科ふっか／整痛院ふっか 東京駅院 出店計画 ／ 日本橋WASAMIビル

5階 平面計画図（施術室10室・フリースペース・スタッフ休憩室） S=1/100

基本計画（出店企画書添付資料） 2026.10


No.A-03 A3

外観立面図・サイン計画図（正面 Y1通り）

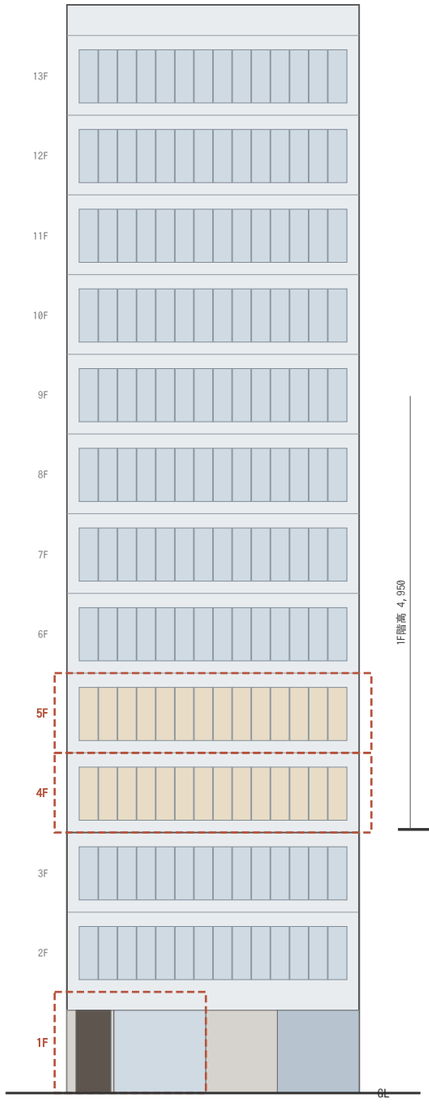

正面全体立面（Y1通り・模式）

S=1/300　赤破線＝当社区画

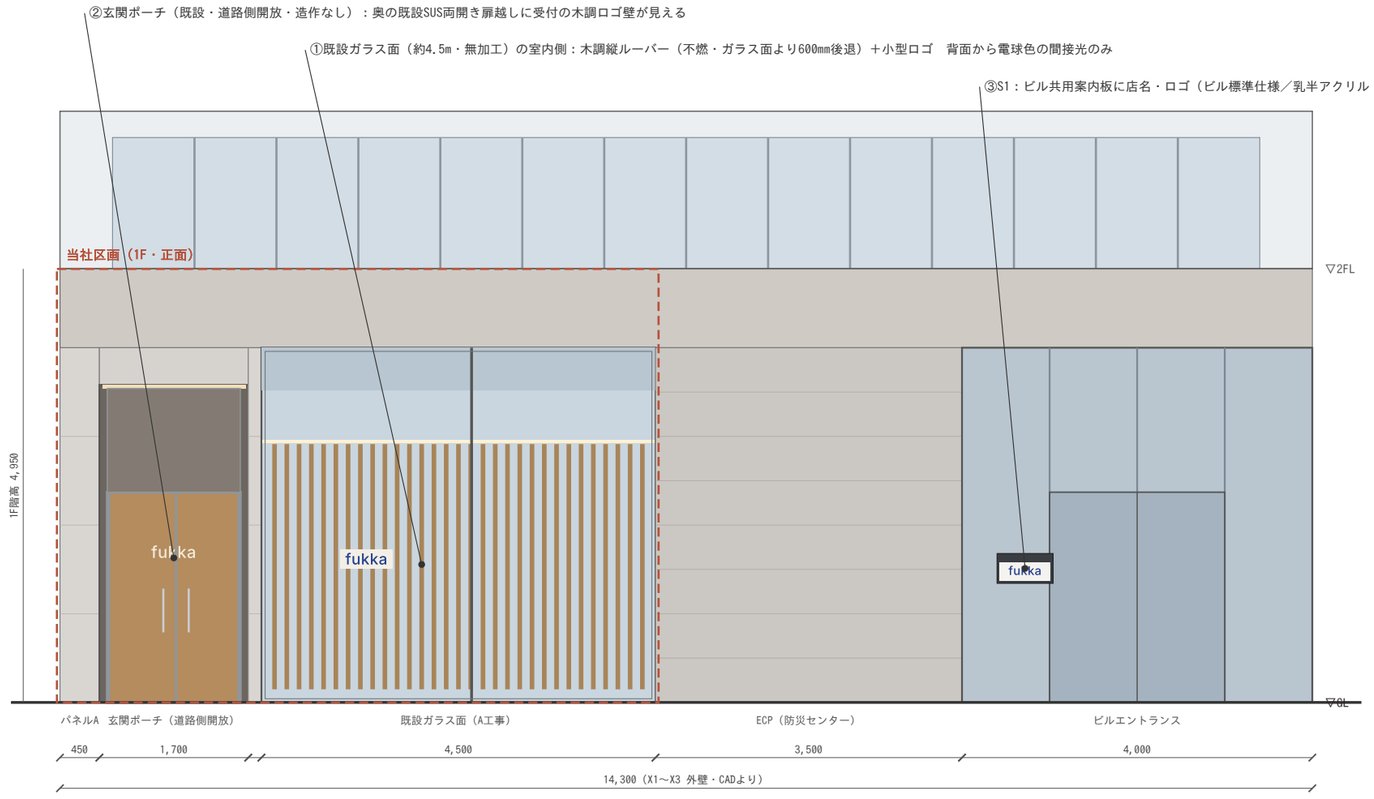

1階 正面部分立面図（サイン位置・使用素材）

S=1/70

サイン詳細（ビル指定仕様に準拠）



S1　W640×H340

ビル共用案内板（エントランス）
乳半アクリル＋ロゴ出力・LED内照
表示：ロゴのみ／約0.14㎡



S2　W300×H300

X1通り側・ビル指定位置
マットアクリル＋ダイノック
白切文字／約0.09㎡

外装サイン方針

（貸主ご意向：落ち着いた外観）


- 突出・袖看板、壁面大型看板は設けない
- ガラス面のフィルム・ポスター広告なし
- S1・S2以外の屋外サインなし
- 点滅・映像・赤色光・ネオン不使用
- 店名・ロゴのみ（価格・施術内容の広告なし）
- 電球色2700〜3000Kの間接光、調光・タイマー
- ガラス面から600mm以上離隔、既設サッシ無加工
- 玄関ポーチは既設のまま（造作・看板なし）
- 表示面積 合計約0.35㎡（上限10㎡）
- 4・5F窓：防炎ロールスクリーンのみ

・1F階高4,950は貸主CAD（展開図 1FL→2FL）より。基準階階高3,900、2F以上の外装は完成予想CGからの模式表現。
・サイン位置・形状はビル側指定（内装マニュアル7-(6)）に準拠。最終仕様は運営管理者と協議のうえ承認を得る。
・正面の当社区画は玄関ポーチ（道路側開放）と既設ガラス面 約4.5mを含む約6.8m（1階 98.36㎡区画・CADより）。ガラス面・サッシは無加工、フィルム等は貼らない。


整形外科ふっか／整痛院ふっか 東京駅院 出店計画 ／ 日本橋WASAMIビル	
外観立面図・サイン計画図 基本計画（出店企画書添付資料）　2026.10	S=1/300・1/70 No.A-04　A3

1F 玄関ポーチ・道路側ガラス面 詳細図


平面詳細　S=1/40

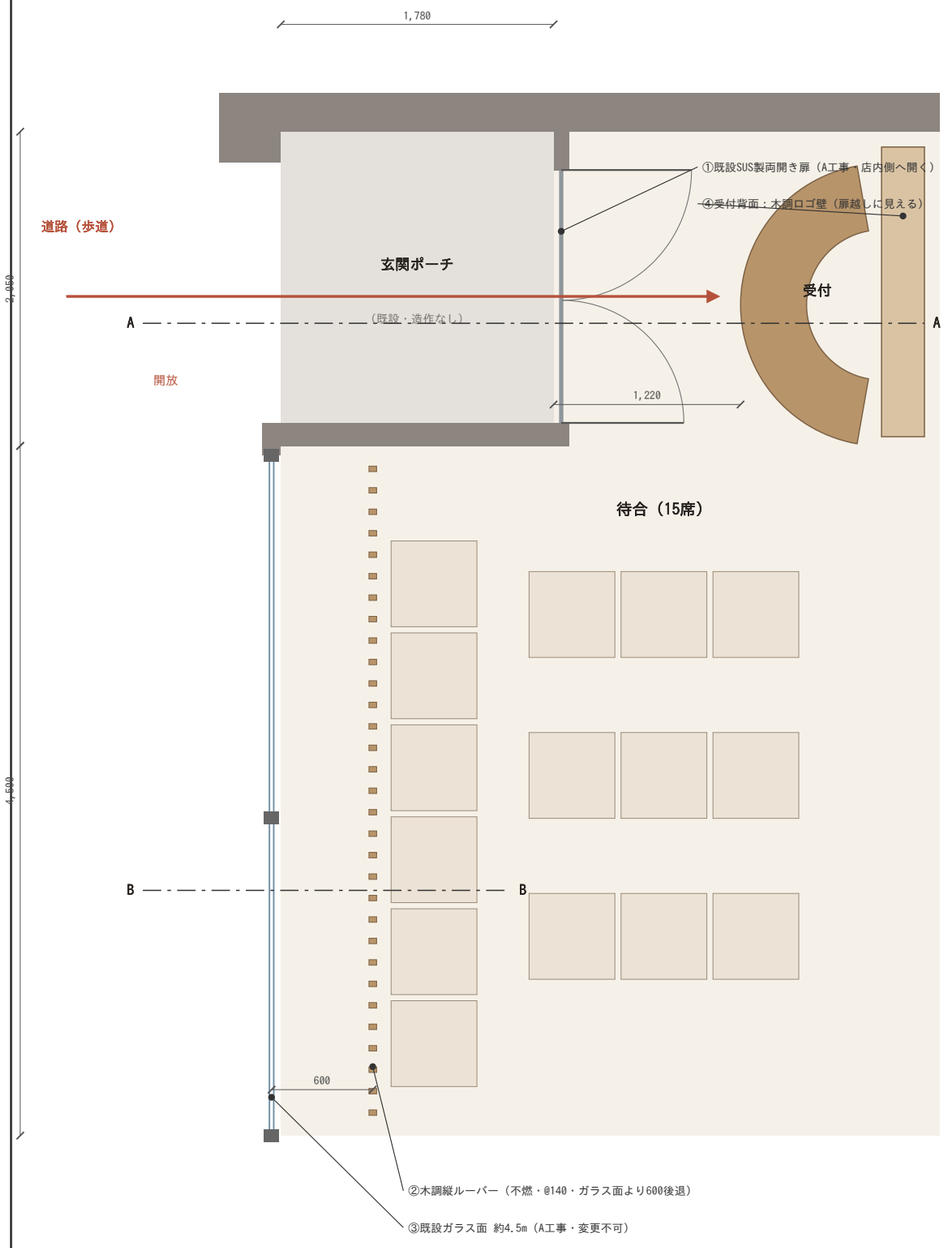


断面 A-A（玄関ポーチ）S=1/50

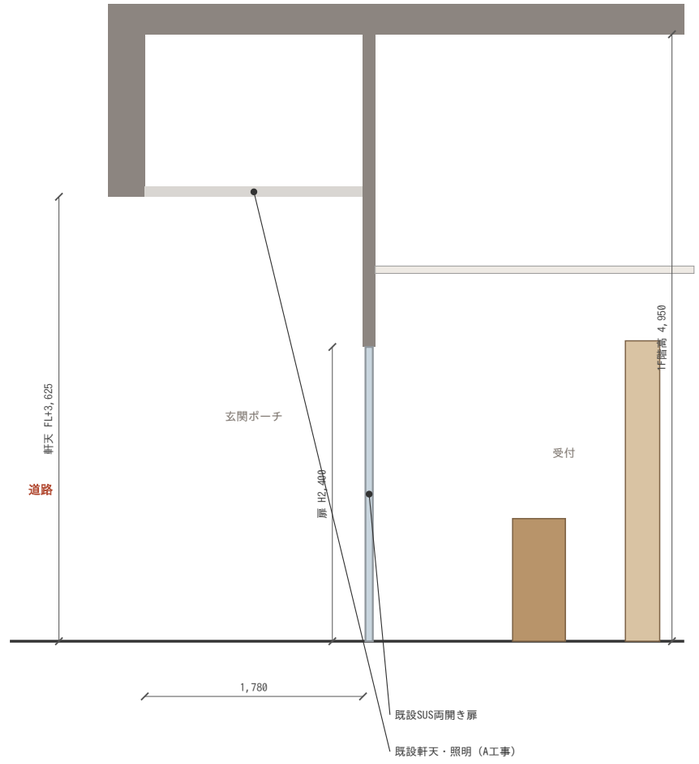

断面 B-B（道路側ガラス面）S=1/50

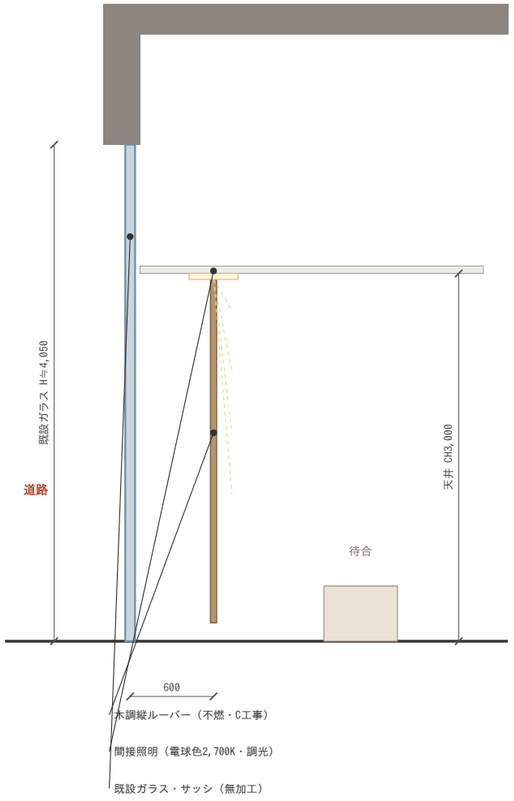

正面（道路から見た当社区画）S=1/80

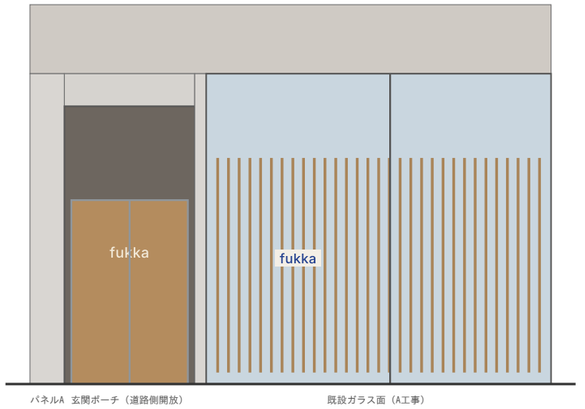


ポーチ奥：既設SUS扉越しに受付の木調ロゴ壁
ガラス面：600mm奥の木調縦ルーバー＋小型ロゴ
看板・ガラス面への貼物なし
→ 立面図 A-04・外装イメージ P.8 と同一

・玄関ポーチは区画内（道路側開放・扉なし）。床・壁・軒天・奥の両開き扉（SUS製）は既設（A工事）のまま使用し、ポーチ内に造作・看板は設けない。
・道路側ガラス面（約4.5m）・サッシは既設（A工事）で変更不可。室内側にガラス面から600mm後退した木調縦ルーバー（不燃・C工事）を設け、外からの視線をやわらげる。
・受付カウンターは扉の内側1,220mmを空けて配置（扉は店内側へ開く）。ロゴは受付背面の木調壁に表示し、扉越しに見える控えめな表示とする。
・寸法は1F CAD（貸主）からの読取り値。ポーチ床の段差・勾配（FL-70〜±0・スロープ1/26）、軒天高さ（FL+3,625）は既設図による。実施設計時に確定。

整形外科ふっか／整痛院ふっか 東京駅院 出店計画 ／ 日本橋WASAMIビル

1F 玄関ポーチ・道路側ガラス面 詳細図	S=1/40・1/50
基本計画（出店企画書添付資料）　2026.10	No.A-05　A3

外装イメージ EXTERIOR IMAGE

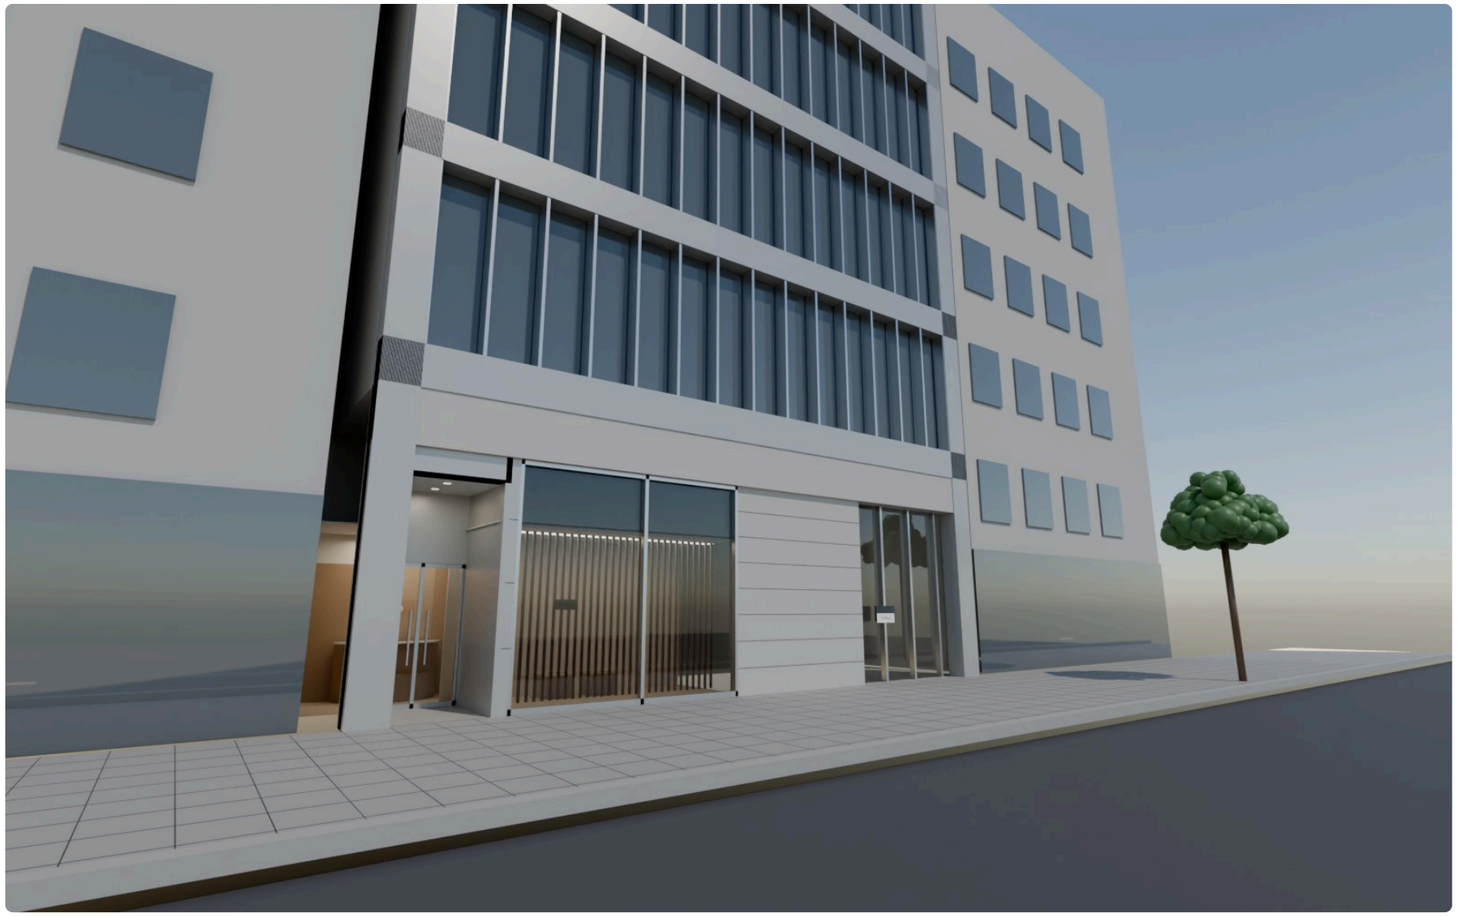

外装　正面（Y1通り）外観イメージ

ビル既設の外装・玄関ポーチ・ガラス面はそのまま。道路側ガラス面（約4.5m）の内側600mmに木調縦ルーバーを設け、小型ロゴとビル共用案内板（S1）のみ表示。突出看板・ガラス面への貼物はありません（立面図 A-04・詳細図 A-05 と同一）。



外装　1F 玄関ポーチまわり

道路側に開いた既設の玄関ポーチ（造作なし）。奥の既設SUS両開き扉越しに受付の木調ロゴ壁が見える、控えめで落ち着いた表情です。



正面全景

4・5F窓面は内側の防炎ロールスクリーンのみで、サイン表示はありません。

内装イメージ　1階（受付・待合・診察室・処置室）　INTERIOR IMAGE 1F



1F　1F 受付・待合

玄関ポーチの既設扉を入ると正面に円形受付（扉から1,220㎜）。銀座院と同じ木の天井リングとロゴ壁。道路側の大きなガラス面（約4.5m）は、600㎜内側の木調縦ルーバーで外からの視線をやわらげ、やさしい光を取り込みます。







1F　廊下と診察室・処置室

待合から幅1,200㎜の廊下で、北側に診察室4室・南側に処置室3室。館内側出入口からも直接入れます。



1F　診察室（各約5.6㎡）

診察デスクとモニター、患者いす、診察ベッド、手洗い器。4室とも同じ仕様です。

内装イメージ　4階（受付ロビー・更衣室・施術室）　INTERIOR IMAGE 4F



4F　4F 受付ロビー

EVホールから続く柱・壁のない開放的なロビー。中央に大きな円形受付、木の天井リング、棚とロゴ壁で銀座院の雰囲気を再現。待合いすはゆとりをもって配置。




4F　EVホール側から見た受付

エレベーターを降りて正面に受付が見える配置です。





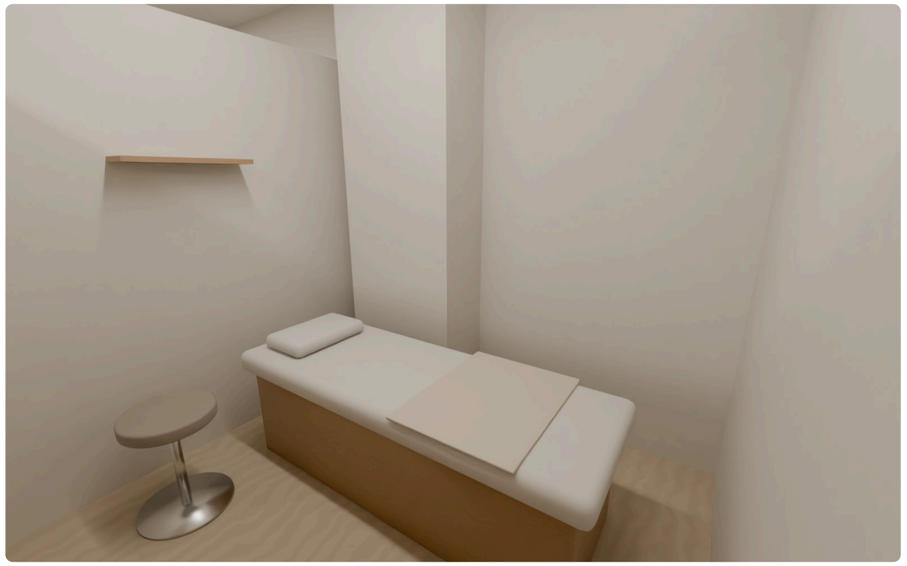

4F　施術室（約6.6㎡・約4畳）

ベッド・スツール・荷物かご・フック。木目の引戸で統一（窓なし）。

内装イメージ　5階（施術室・フリースペース・スタッフエリア）

INTERIOR IMAGE 5F



5F **5F フリースペース**

施術前後の待合・カウンセリング・セミナーに使えるラウンジ。造作ベンチと丸テーブル、銀座院と同じ素材と色。



5F **スタッフ休憩室（約18㎡）**

道路側の窓に面した明るい休憩室。ミニキッチン・冷蔵庫付き。スタッフ更衣室（男女）・物品庫も5階に集約。



5F **5F 俯瞰**

施術室10室／フリースペース／スタッフ休憩室・更衣室／物品・リネン庫

収支計画と賃料比率について　FINANCIAL PLAN

8,480万円
最終月商（年商 約10億1,700万円）


約11%
賃料比率（最終月）

94%
粗利率（自費100%）

約37%
営業利益率（最終月）

① 超好立地による「広告費の代替」

JR東京駅（22番出口）徒歩1分・日本橋駅徒歩4分。日本有数のターミナル駅の通勤・出張・来訪動線上にあり、「通いやすい場所にある」こと自体が最大の集客力になります。慢性痛のコース施術は通院の継続が前提のため、駅至近の立地は継続率・紹介にも直結します。看板を大きく出さずとも駅前の認知と紹介・リピートで集客でき、**広告宣伝費を売上比 約4%**に抑える計画です。賃料と広告費を合わせた「集客コスト」で比べると、一般的な自費クリニックより低い水準です。

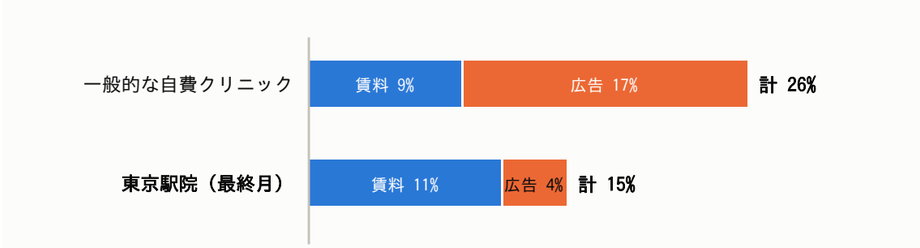

売上に対する比率（集客コスト＝賃料＋広告宣伝費）

② 自費診療・自費施術による高い粗利率


1F整形外科（自費診療：診察3,000〜9,000円・処置）と、4・5F整痛院のコース制施術（痛み消失コース6か月88万円・理想の体コース12か月132万円）はすべて自費のため、保険点数に左右されず**粗利率は約94%**。原価は消耗品・医療材料程度で、売上増加分の大半が利益に残る構造です。

③ 賃料負担に耐えられる収益構造


固定費（人件費の固定分・賃料・広告・その他）に対する損益分岐売上は**月 約4,696万円**。最終月商8,480万円はその約181%で、売上が約45%下振れしても赤字にならない余裕があります。開業6か月目に単月黒字化、2年目以降は賃料比率 約13%以下、営業利益率 約31%以上で推移する計画です。

※賃料・共益費は借室申込書の条件（1階 97,000円/坪、4・5階 45,000円/坪、共益費 3,000円/坪）で 約965万円/月（最終月商比 約11%）。人件費等の固定費は月商規模に応じて増員する前提。数値はすべて概算。業界平均は自費クリニックの一般的な目安値。

月商・営業利益の推移（開業から36か月）

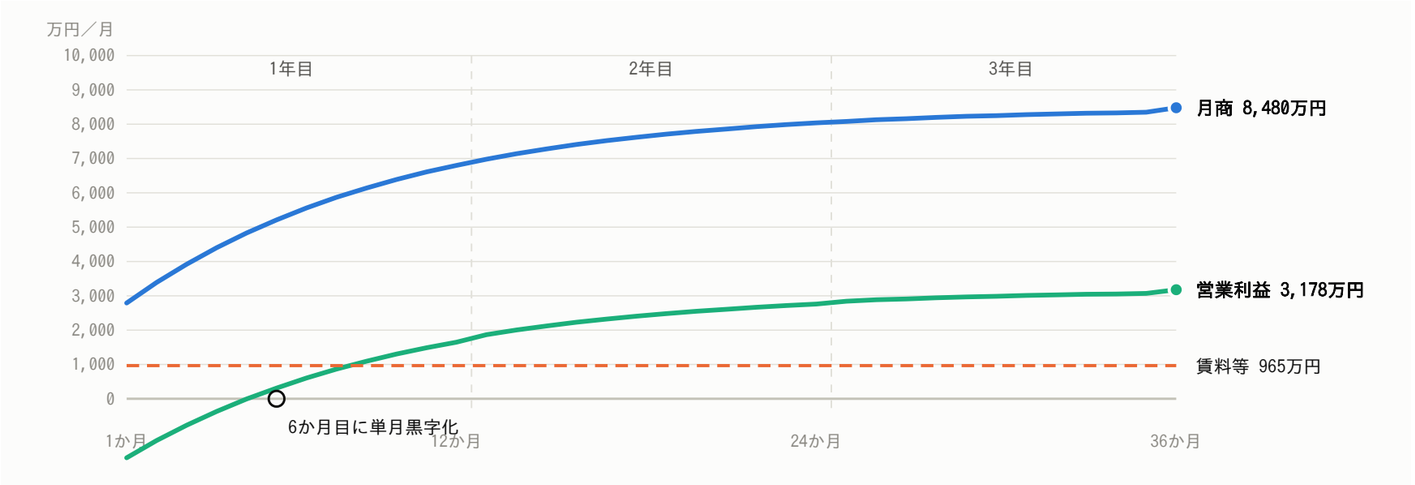

年次の売上・費用・営業利益（月平均）

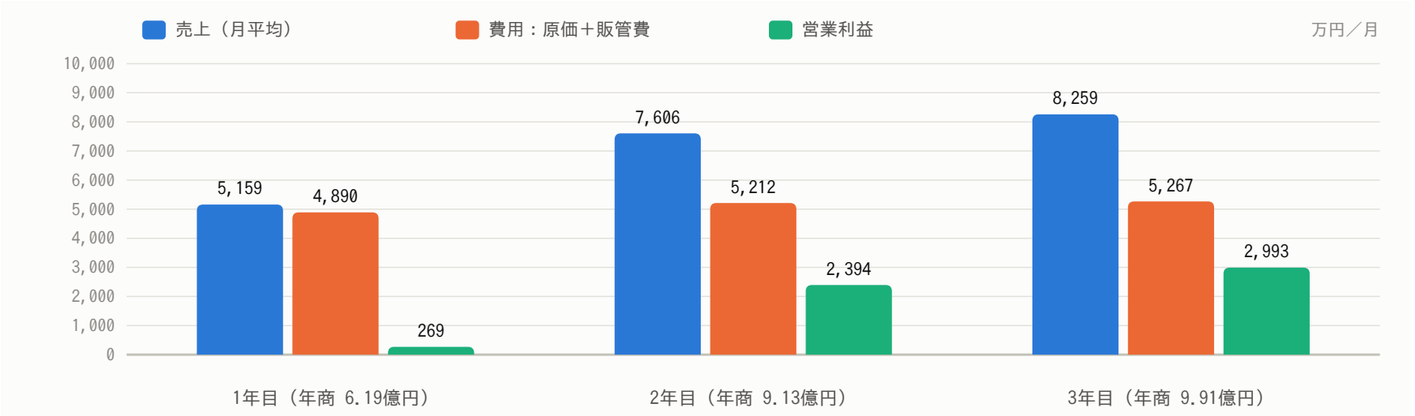

万円／月（年平均）	1年目	2年目	3年目	最終月
売上高	**5,159**	**7,606**	**8,259**	**8,480**
売上原価	310	456	496	509
人件費	2,153	2,348	2,401	2,418
賃料・共益費	965	965	965	965
広告宣伝費	450	380	330	330
その他販管費	1,013	1,062	1,075	1,080
営業利益	**269**	**2,394**	**2,993**	**3,178**
営業利益率／賃料比率	5%／19%	31%／13%	36%／12%	37%／11%

銀座院のご紹介（整痛院ふっか） GINZA CLINIC


銀座院 待合・受付（実写）


受付カウンター


個室（施術・カウンセリング）


カウンセリング


施術・説明


講演・セミナー活動

3万件超
グループ累計施術件数

9院
全国展開（福岡・東京ほか）

2016年
開業（2023年 法人化）

2025年
銀座 新モデル大型院を開院

腰痛・坐骨神経痛など慢性的な痛み・しびれに特化した「整痛院」。2025年には大阪・関西万博のステージで「整痛」の取り組みを講演。 東京駅院では、銀座院の施術モデルに**整形外科の医療フロア（診察室4室・処置室3室）**を加え、診察から施術まで一貫して提供します。 東京駅院の内装は、写真の銀座院（白い塗り壁・木目・ベージュのカーペット・円形受付）をそのまま踏襲します。

会社・銀座院の概要（公開情報）

ブランド	整痛院ふっか（痛み・しびれ専門）
運営	株式会社ふっか（代表取締役 松田 圭太・理学療法士）
沿革	2016年8月 開業（福岡）／2023年6月 法人化
店舗	全国9院（2025年5月時点）
銀座院	2025年6月6日開院　東京都中央区銀座3-13-19 3F（東銀座駅 徒歩約2分）
営業	9:00〜21:00（不定休）・完全予約制
施術	独自のMSMメソッド（手技・運動療法・認知行動療法の考え方）
料金	初回 12,000円（税込）／初回約120分・2回目以降約30分

東京駅院のイメージ（参考）



銀座院の内装パース。東京駅院も同じトーン＆マナーで計画。

写真・情報出典：整痛院ふっか公式サイト（fukka.jp）、整痛院ふっか銀座院ページ、PR TIMES（株式会社ふっか プレスリリース）。数値は公表時点のもの。

仕上表・ビル規定への対応 FINISH SCHEDULE / COMPLIANCE

仕上表（概略・基本計画段階）

部位	仕上	備考
床	タイルカーペット（防炎品・防炎表示付、ベージュ系・銀座院同等柄）／処置室：ビニル床シート	4・5F：既設OAフロア（h=100）上に施工／1F：コンクリート直（FL-300）のため置床で嵩上げ
巾木	ソフト巾木 H60（ベージュ）	
壁	軽量鉄骨下地＋石膏ボード（不燃）AEP塗装（白・塗り壁調）／受付背面：木目調不燃化粧板	施術室間仕切は上部開放の欄間式（欄間 h=500）
天井	4・5F：既設天井（CH2,800）／1F：直天（想定FL+3,700）のため石膏ボード天井を新設（CH約3,000）　受付上部：木目調リング（不燃）	既設の感知器・スプリンクラー・非常照明の機能を妨げない
建具	施術室：木目調不燃化粧板 引戸 W900×H2,100／診察室・処置室：木目調不燃化粧板 引戸／1F玄関：既設SUS製両開き扉（A工事）をそのまま使用	鍵1本をビル側へお預け。B工事の扉は室内側へ内開き
家具	受付カウンター（木目＋白天板）、待合いす（ベージュ張地・木脚）、施術ベッド	防災設備の機能を妨げない配置
照明	LEDライン照明・ダウンライト（電球色〜温白色 3,000〜3,500K、調光）	4・5F電気容量：1Φ約100VA/㎡、3Φ約200VA/㎡（募集資料）
カーテン等	4・5F道路側窓：防炎ロールスクリーン（アイボリー）／1F道路側ガラス面：木調縦ルーバー（不燃・ガラス面から600㎜後退）	防炎物品（防炎ラベル縫付）。ガラス面へのフィルム等は貼らない
医療設備	1F 診察室4室・処置室3室：全室に手洗い器（給排水はB工事で分岐）、診察台・処置ベッド・医療機器用コンセント	感染性廃棄物は許可業者へ処理委託

内装マニュアル（ビル規定）への対応

床荷重	1〜3F 5,000N/㎡、4・5F 3,000N/㎡（室内全体の荷重制限は別途）。1Fは重量物を置かない計画
間仕切	不燃材を使用。上部開放の欄間式（欄間 h≧500）とし、防災設備の追加が必要な場合はB工事で対応
廊下幅	両側に居室が面する通路は有効1,600㎜、その他の廊下は1,200㎜以上を確保（建築基準法施行令119条）
避難経路	2〜5F：EVホールから避難階段附室まで廊下状に整備。当計画は廊下・通路で特別避難階段・共用トイレに直結。EVホール入口の防火扉の開閉を妨げる造作・什器なし
ファサード・サイン	既設サッシ・ガラス・1F玄関ポーチは無加工（ポーチ内に造作・看板なし）、ガラス面から600㎜程度離隔。サインはビル指定位置（S1・S2）のみ、店名・ロゴに限定。点滅・映像・赤色光・露出ネオン不使用、表示面積10㎡以下
電気・空調	設定容量内で計画（設定容量を超える電源増設・保安電源の増設は不可）。空調吹出口・吸込口の機能を妨げない
特殊設備	騒音・振動・熱を発生する機器（空調室外機等）はビル側の承認を得て設置。躯体のはつり・ホールインアンカーは原則不可
給排水	4・5F：給水 PS内バルブ止め（40A）、排水 区画内スラブ上ころがしキャップ止め（100A）。漏水対策（防水・漏水検知）を指示に従い実施
点検口・収納	共用配管・配線部に点検口を設置。共用倉庫・従業員ロッカーはないため、店舗内（5F）に確保
用途	誘導用途区画（日本橋・東京駅前地区）のため、診療所・施術所としての用途適合性を事前に確認
提出図書	B工事指示書・基本設計図書：着工2.5か月前（B工事見積は1か月）／工事申請書・実施設計図：着工1か月前／竣工図：竣工後1か月以内

※出典：内装マニュアル（2026年8月7日発行）、募集資料。本資料は出店審査用の基本計画です。図面寸法は募集図面・1F CADからの読取り値で、実施設計時にビル側の白図・設備図に基づき確定します。パースはイメージで、実際の仕上・家具とは異なる場合があります。

整痛院ふっか

お問い合わせ・詳細はこちら

https://s.fukka.jp/l/u/EhhbGg18mMxd4lXL